



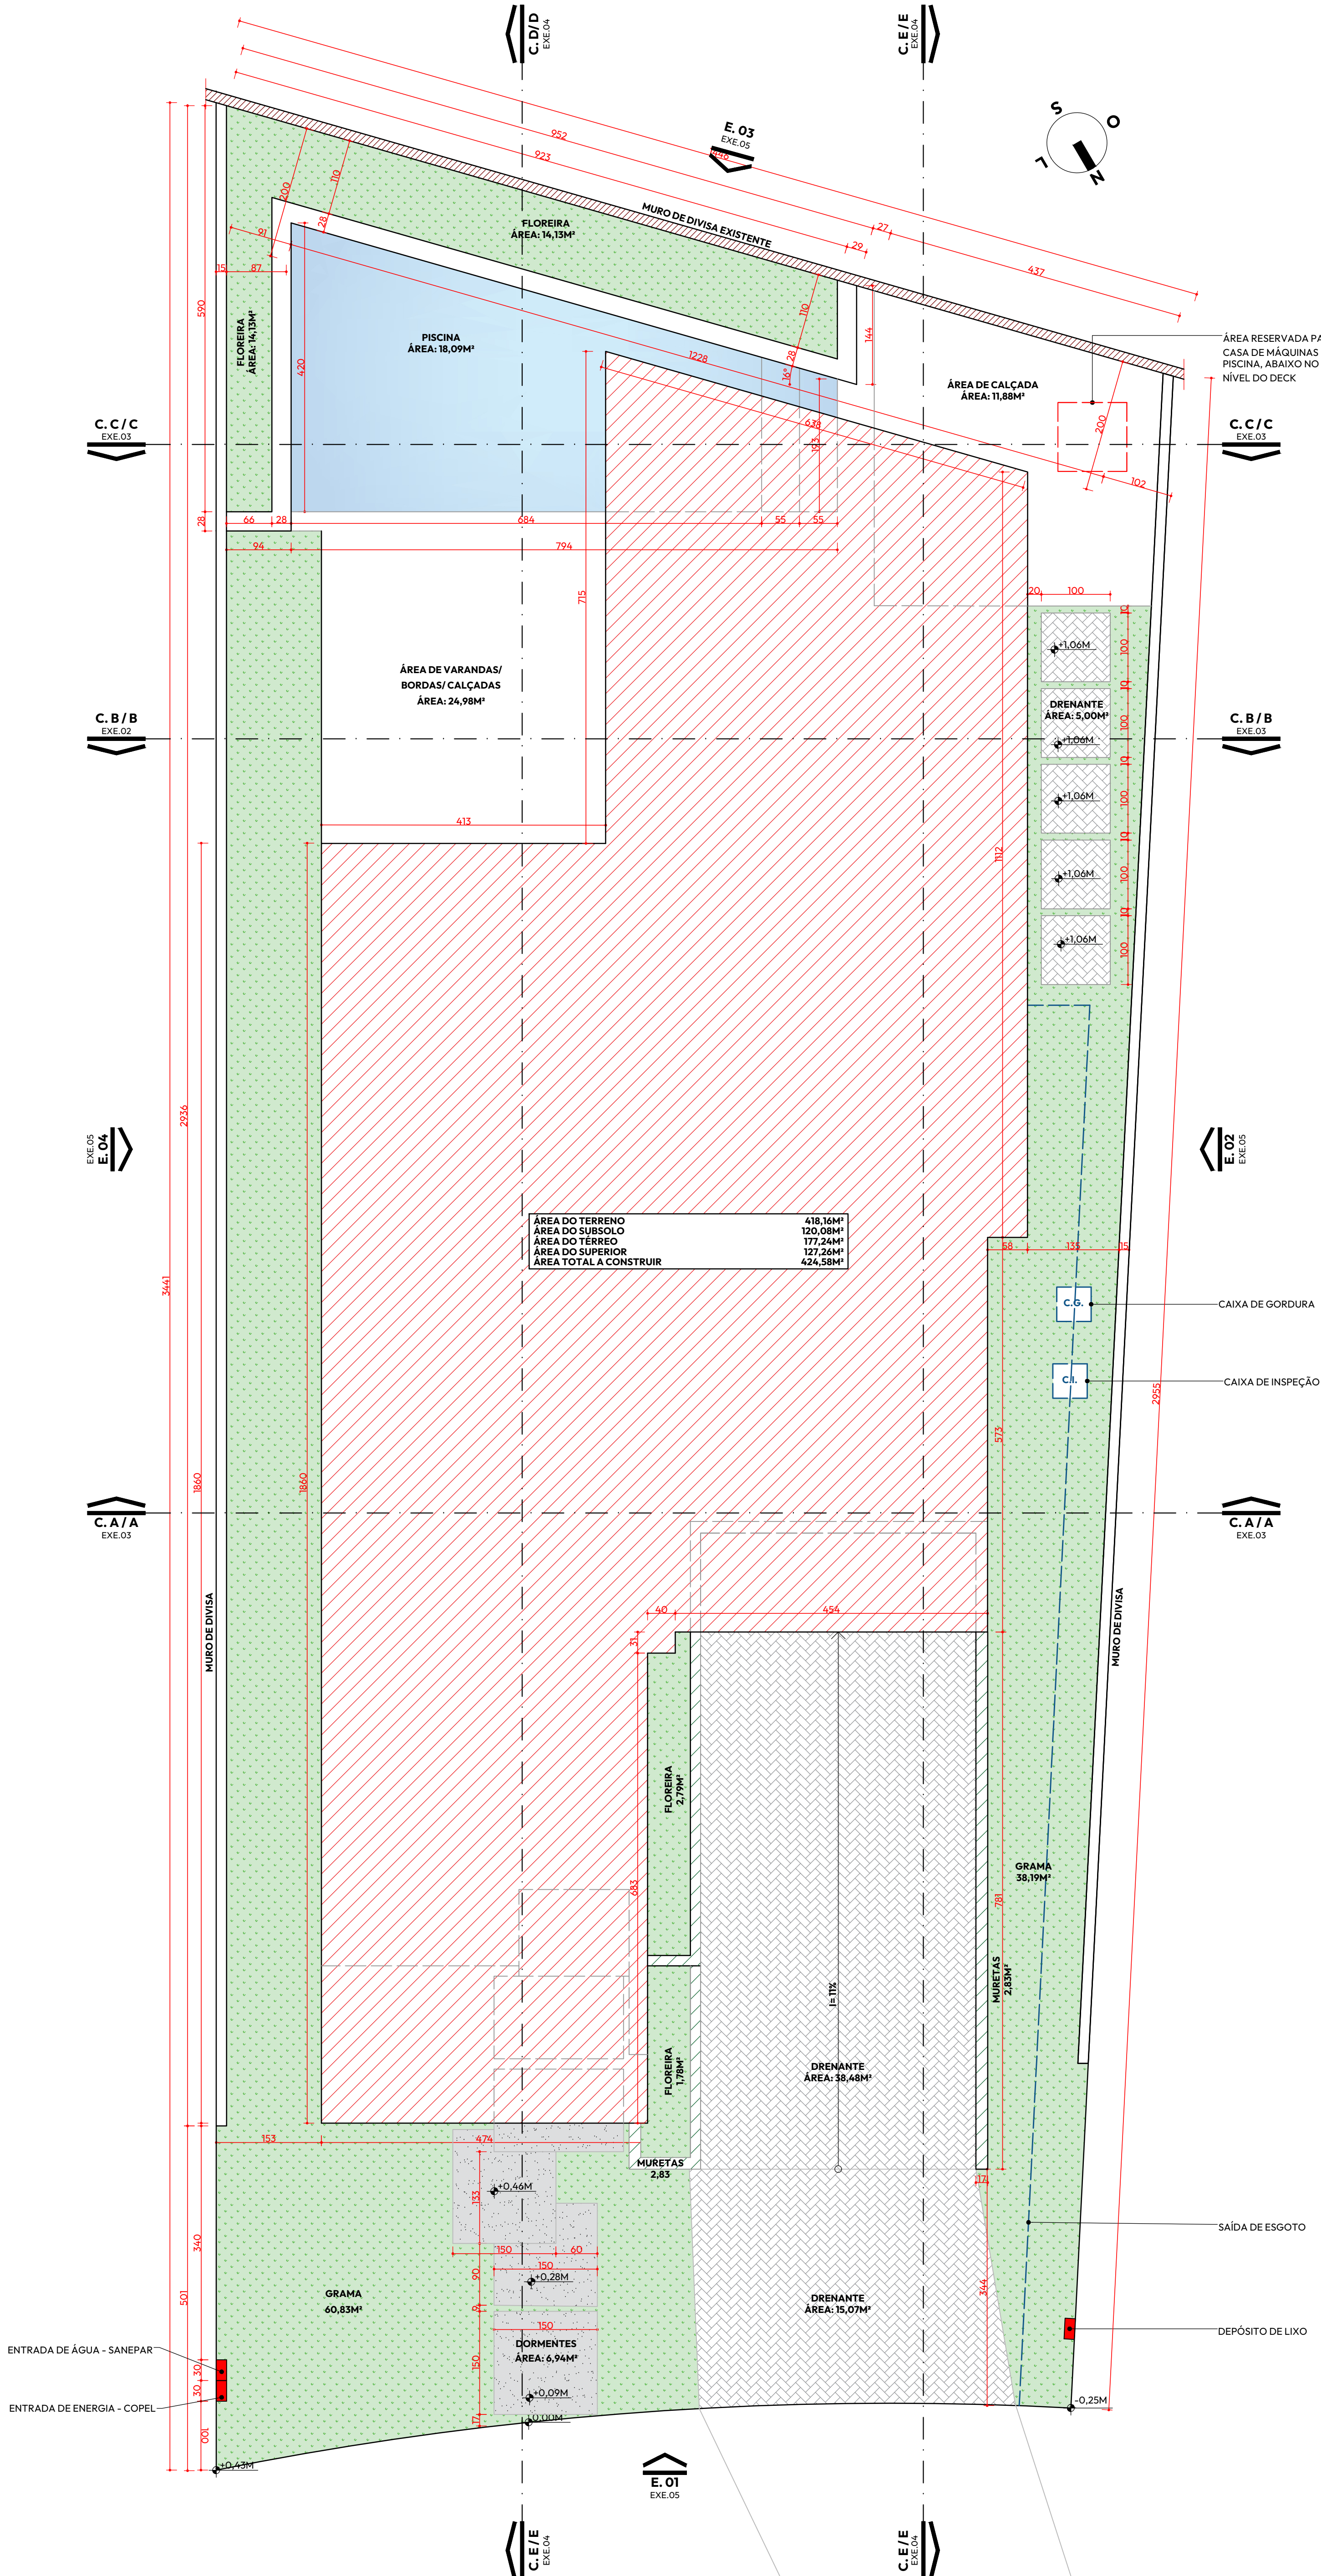

01 PLANTA BAIXA IMPLANTAÇÃO
ESCALA: 1/50

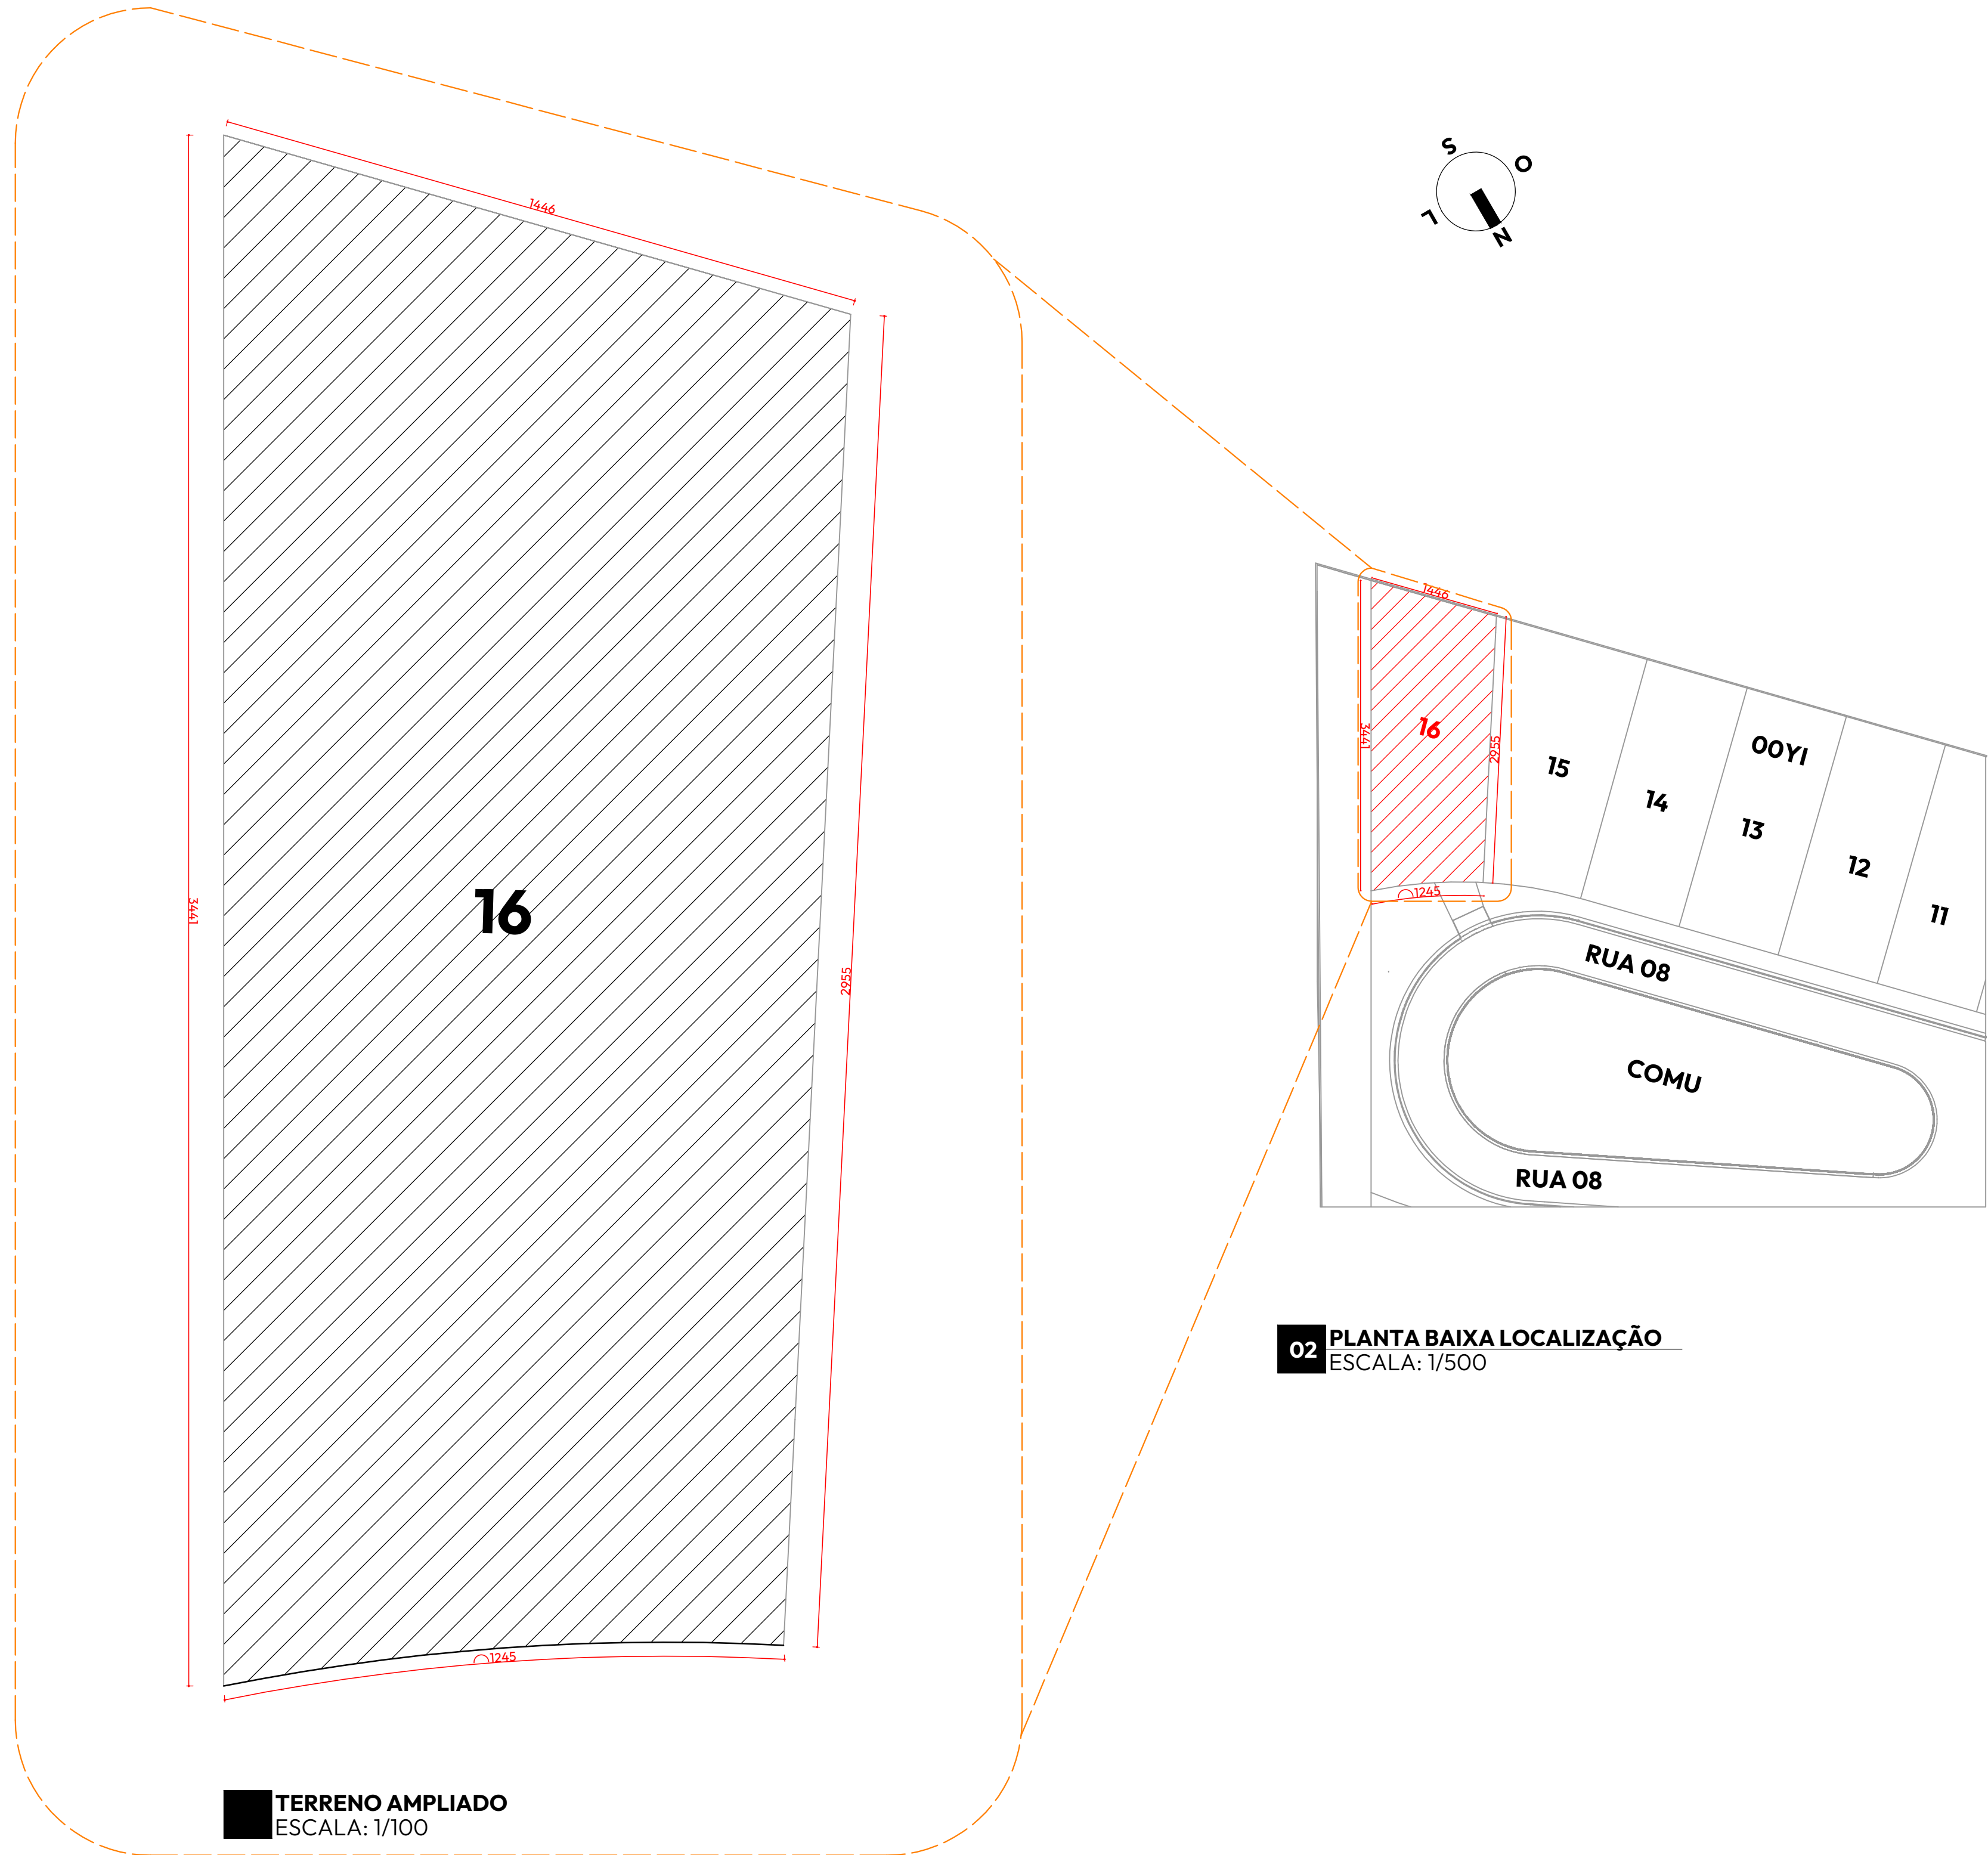

02 PLANTA BAIXA LOCALIZAÇÃO
ESCALA: 1/500

OBSERVAÇÕES DIVERSAS

- CONSIDERAR NICHOS PARA BANHEIRA E ARMÁRIOS E AÉREOS.
- CONSIDERAR NICHOS PARA LAVÁ-LOUÇAS ENCOIMAS E ESPAÇOS GOURMETS.
- CONSIDERAR REBAIXO DE 2 CM EM ÁREAS DE BOX DOS BANHEIROS.
- CONSIDERAR VENTILAÇÃO E CONTRAVENTURA EM TODAS AS ABERTURAS.
- CONSIDERAR IMPERMEABILIZAÇÃO EM BANHEIROS, BALCÕES, LAJES APARENTES, SACADAS, FLOREIRAS E DEMAIS ÁREAS INDICADAS PELO RESPONSÁVEL PELA EXECUÇÃO.
- CONSIDERAR RODAPÊ EMBUTIDO EM TODOS OS PAVIMENTOS.
- CONSIDERAR INCLINAÇÃO DE NO MÍNIMO 2% E DRENOS EM ÁREAS DE LAJES IMPERMEABILIZADAS E TERRAÇOS.
- DEIXAR ESPERA ELÉTRICA PARA ILUMINAÇÃO DE JARDIM.
- QUALQUER DIVERGÊNCIA DEVE SER COMPATIBILIZADA ANTES DA EXECUÇÃO.
- OS MUIROS DE DIVISA DEVEM INICIAR A PARTIR DA FAIXA DE RECUE FRONTAL (3 METROS).
- A ALTURA MÁXIMA DO ARRIMO NÃO DEVE ULTRAPASSAR 2 METROS.
- A TOPOGRAFIA DA CALÇADA DEVE PERMANECER NO PERFIL NATURAL.
- A CALÇADA DEVE SER EXECUTADA CONFORME PADRÃO ESTABELECIDO PELO CONDOMÍNIO.
- TODAS AS CONDENSADORAS DEVEM SER POSICIONADAS NA SACADA TÉCNICA AJUNTO AO TELHADO. É ESTRITAMENTE PROIBIDO O POSICIONAMENTO EM FACHADAS.

LEGENDA DE CORES IMPLANTAÇÃO - PAVIMENTO TERREO

PADRÃO	DESCRIÇÃO
	PISCINA
	GRAMA/ FLOREIRAS
	DRENANTE
	CONCRETO/ PORCELANATO
	MURETAS
	CONSTRUÇÃO

REVISÕES:

REVISÃO	DATA	DESCRIÇÃO	DESENHO
R02	29/08/25	CORREÇÃO DO QUADRO DE ESTATÍSTICAS	JOSE
R03	29/08/25	CORREÇÃO DO QUADRO DE ESTATÍSTICAS	JOSE
R04	04/02/26	COMPATIBILIZAÇÃO DO PROJETO DE INTERIORES	JOSE

ESTATÍSTICAS:

ÁREA DO TERRENO	418,16M²	TAXA DE OCUPAÇÃO (177,24M²):	42,39%
ÁREA A CONSTRUIR TERREO	177,24M²	COEFICIENTE DE APROVEITAMENTO:	1,0153
ÁREA A CONSTRUIR SUPERIOR	122,26M²	TAXA DE PERMEABILIDADE:	38,94%
ÁREA A CONSTRUIR SUBSOLO	120,08M²	ESCADARIA ENTRADA (CONCRETO)	6,94M²
ÁREA TOTAL A CONSTRUIR	424,58M²	ÁREA DECK	11,88M²
ÁREA PERMEÁVEL	162,85M²	ÁREA PISCINA	18,09M²
SENDO:		ÁREA VARANDA/ CALÇADAS/ BORDAS	26,99M²
GRAMA:	113,15M²	ÁREA MURETAS	2,83M²
DRENANTE (85%)	58,48M²	ÁREA FLOREIRAS NÃO PERMEÁVEIS	4,57M²

ORGÃOS PÚBLICOS:

PROJETO ARQUITETÔNICO RESIDENCIAL

ARQUITETO: GEOVANI CEZAR FELTRINCAU: A130445-3

EXECUÇÃO: MACIEL COSTA DA SILVACPF: 064.664.969-88

PROPRIETÁRIO: MACIEL E FERNANDO

LOCAL: CONDOMÍNIO TERRAS ALPHA CASCAVEL, QUADRA 001, UNIDADE 16

ESCALA: INDICADA

FOLHA: EXE.00

CONTEÚDO: IMPLANTAÇÃO/ LOCALIZAÇÃO

DESENHO: JOSE

DATA: 09/06/25


A APROVAÇÃO DO PRESENTE PROJETO PELA PREFEITURA NÃO RECONHECE A PROPRIEDADE DO IMÓVEL




- | TABELA DE ESQUADRIAS - JANELAS | | | | | | |
|--------------------------------|---------------|---------------|------------------|----------------------|-------|--|
| SÍMBOLO | TAMANHO | VÃO | SISTEMA | ACABAMENTO | QT. | |
| J1 | 250X225/45CM | 250X225/45CM | FIXA | ALUM. PRETO E VIDRO | 01UN | |
| J2 | 280X270/30CM | 280X270/30CM | CORRER 03 FOLHAS | ALUM. PRETO E VIDRO | 01UN | |
| J3 | 100X100/15CM | 100X100/15CM | MALHA 40 FOLHAS | ALUM. P. VIDRO FOSCO | 01UN | |
| J4 | 120X100/15CM | 120X100/15CM | CORRER 02 FOLHAS | ALUM. PRETO E VIDRO | 01UN | |
| J5 | 60X50/15CM | 60X50/15CM | MALHA 40 | ALUM. P. VIDRO FOSCO | 01UN | |
| J6 | 214X213/52CM | 214X213/52CM | CORRER 03 FOLHAS | ALUM. PRETO E VIDRO | 01UN | |
| J7 | 300X323/52CM | 300X323/52CM | CORRER 03 FOLHAS | ALUM. PRETO E VIDRO | 01UN | |
| J8 | 333X323/52CM | 333X323/52CM | CORRER 02 FOLHAS | ALUM. PRETO E VIDRO | 01UN | |
| J9 | 100X120/150CM | 100X120/150CM | CORRER 03 FOLHAS | ALUM. PRETO E VIDRO | 01UN | |
| J10 | 330X323/52CM | 330X323/52CM | CORRER 03 FOLHAS | ALUM. PRETO E VIDRO | 01UN | |
| J11 | 100X120/150CM | 100X120/150CM | CORRER 03 FOLHAS | ALUM. P. VIDRO FOSCO | 02 UN | |
| J12 | 87X213/52CM | 87X213/52CM | CORRER 03 FOLHAS | ALUM. P. VIDRO FOSCO | 02 UN | |
| J13 | 200X213/52CM | 200X213/52CM | CORRER 03 FOLHAS | ALUM. P. VIDRO FOSCO | 01UN | |
| J14 | 400X213/52CM | 400X213/52CM | CORRER 03 FOLHAS | ALUM. PRETO E VIDRO | 01UN | |
| J15 | 414X213/565CM | 414X213/565CM | FIXA - 01 FOLHA | ALUM. PRETO E VIDRO | 01UN | |
| J16 | 105X213/52CM | 105X213/52CM | FIXA - 04 FOLHAS | ALUM. PRETO E VIDRO | 01UN | |
| J17 | 220X80/130CM | 220X80/130CM | CORRER 02 FOLHAS | ALUM. PRETO E VIDRO | 01UN | |

LOCAL: CONDOMINIO TERRAS ALPHA CASCAVEL, QUADRA 00Y1 UNIDADE 16	ESCALA: INDICADA	FOLHA: EXE.01
CONTEÚDO: COBERTURA / SUBSÓCO	DESENHO: JOSÉ	EXE.05
	DATA: 09/06/75	


A APROVAÇÃO DO PRESENTE PROJETO PELA PREFEITURA NÃO RECONHECE A PROPRIEDADE DO IMÓVEL

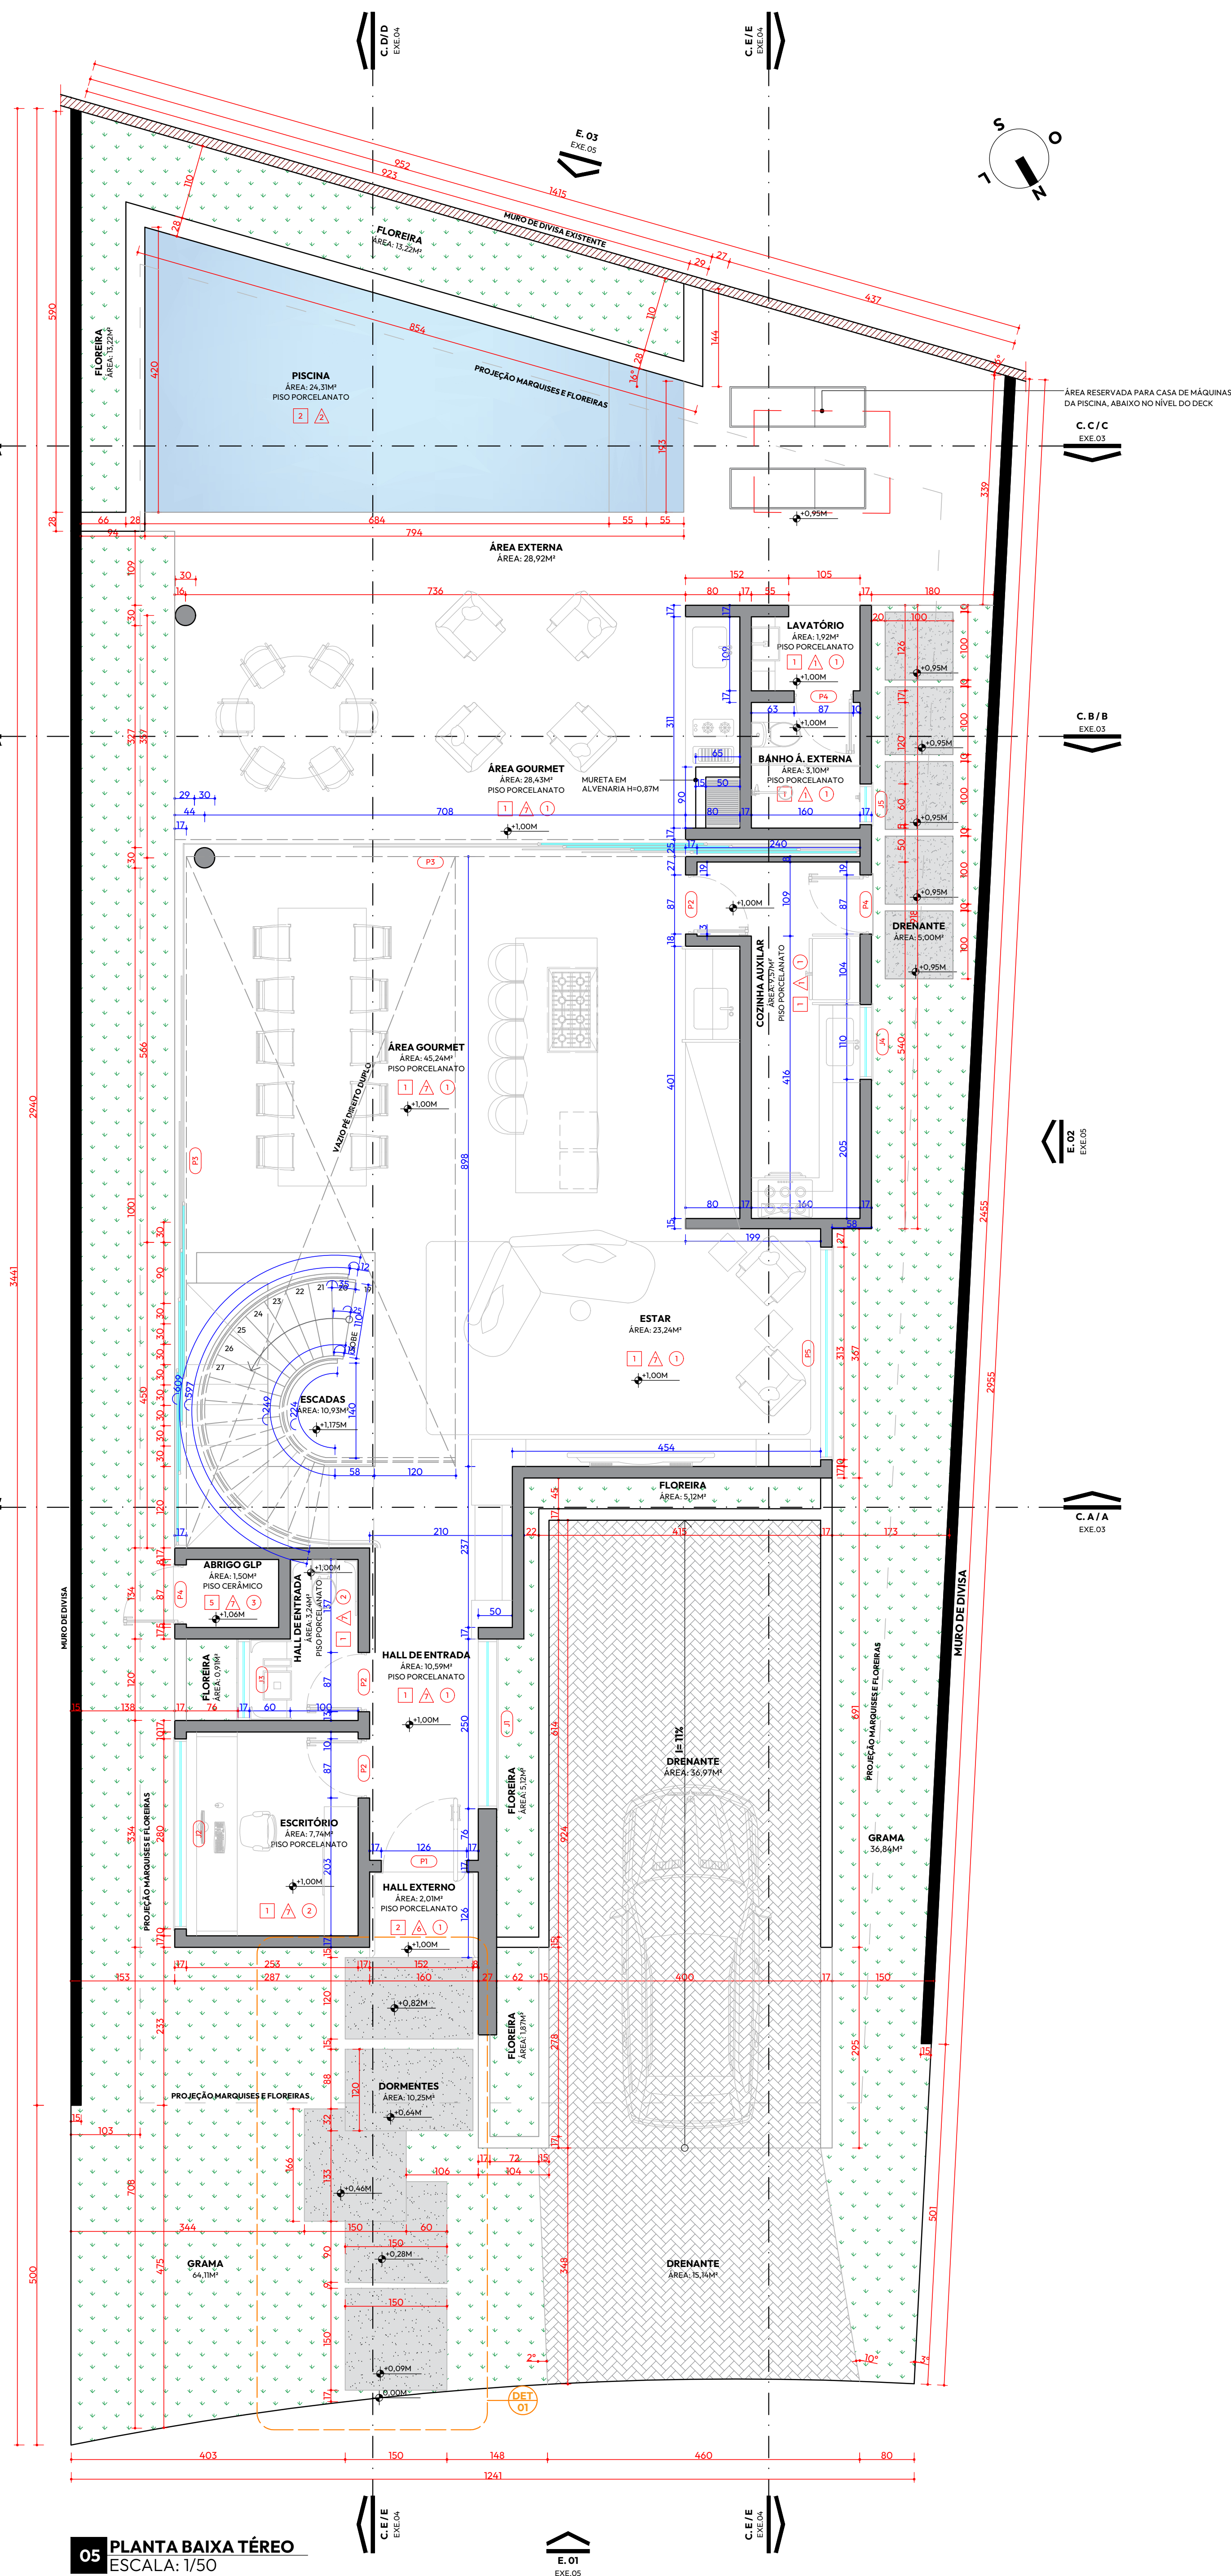


05 PLANTA BAIXA TÉRREO
ESCALA: 1/50

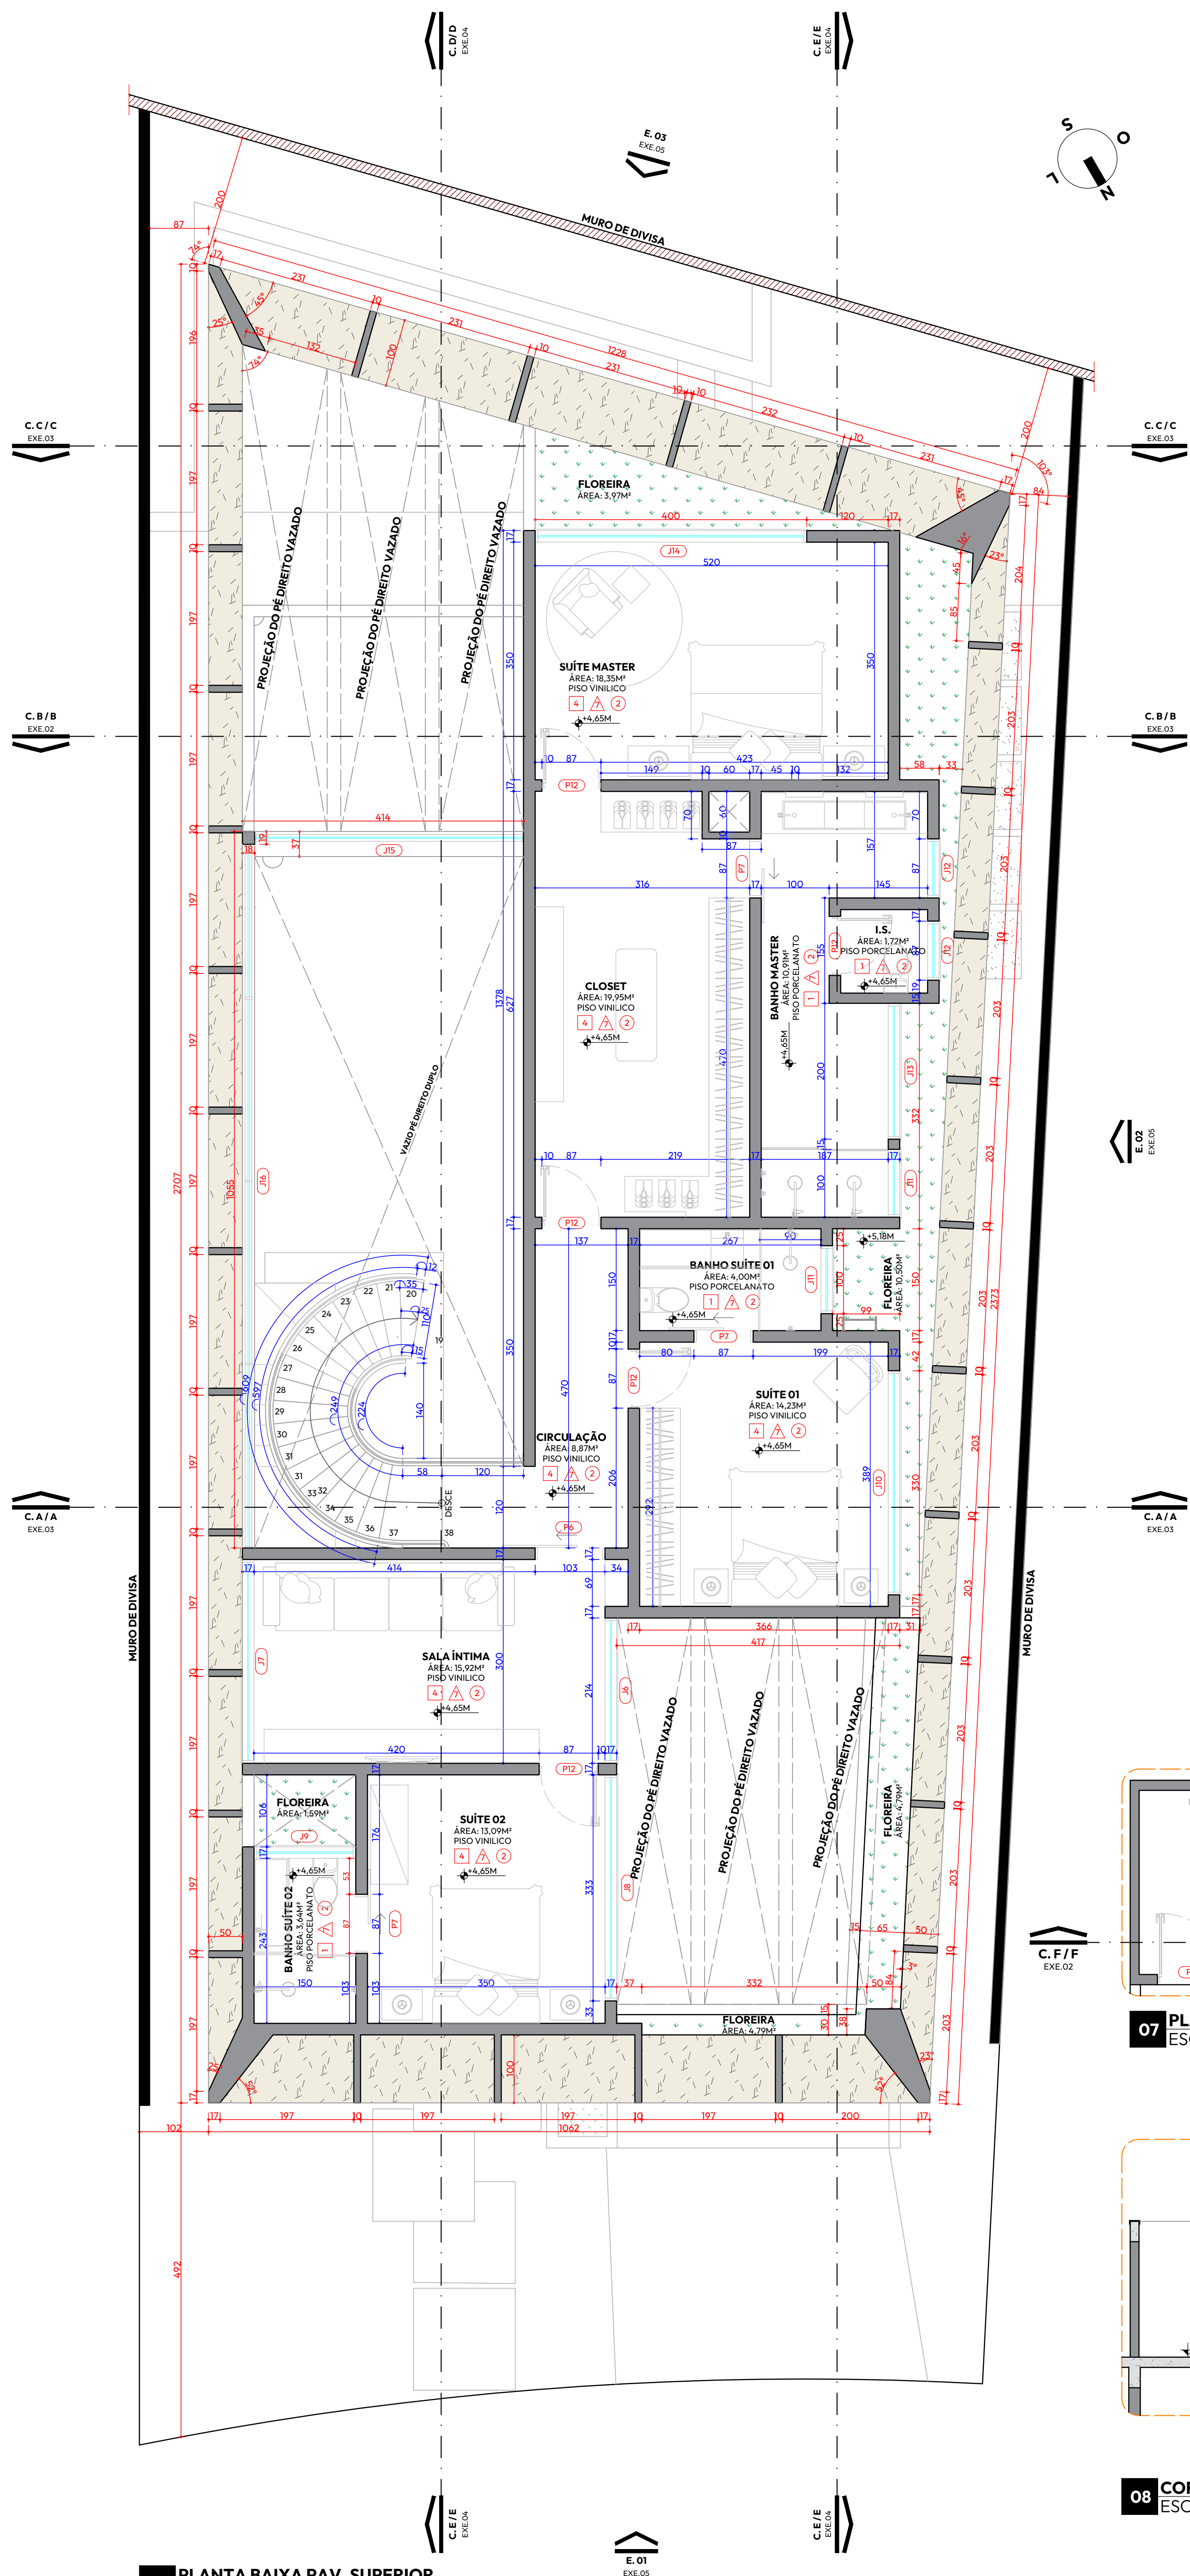


06 PLANTA BAIXA PAV. SUPERIOR
ESCALA: 1/50

 


PERSPECTIVA RENDERIZADA
ESCALA: 1/50

 


PERSPECTIVA RENDERIZADA
SEM ESCALA

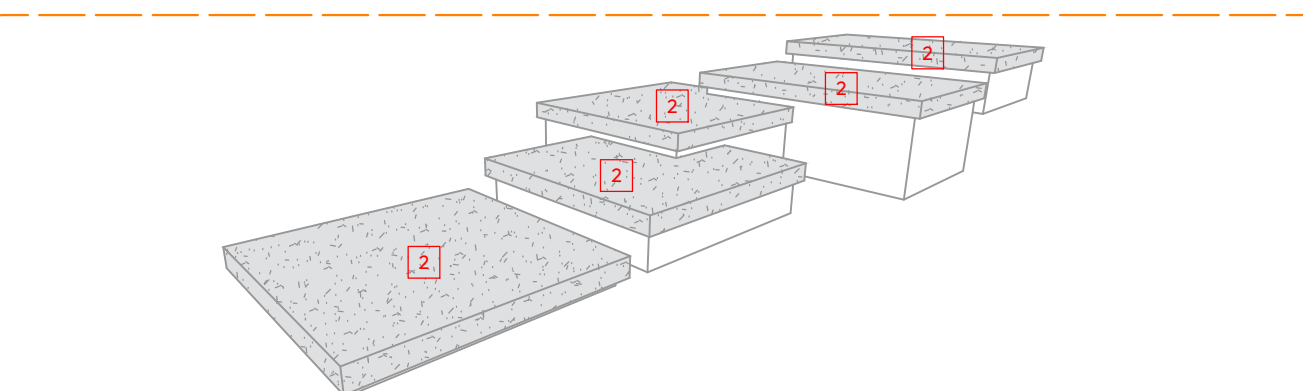


05 PERSPECTIVA DORMENTES ENTRADA
SEM ESCALA

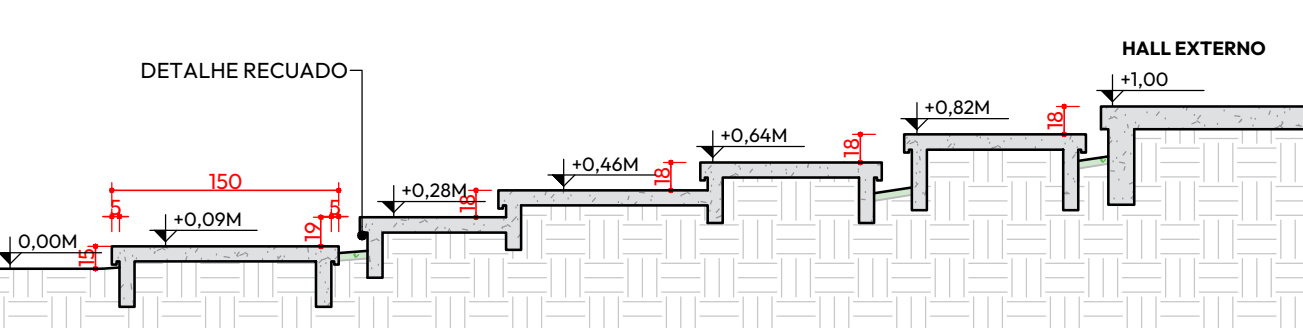

06 DET. EM CORTE DORMENTES ENTRADA
ESCALA: 1/50

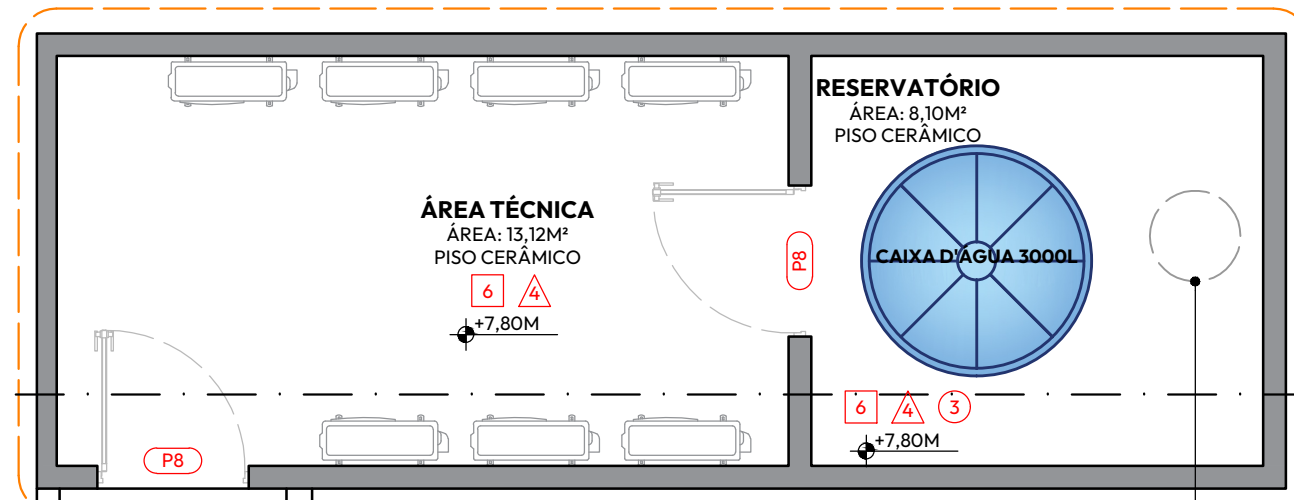


07 PLANTA BAIXA RESERVATÓRIO
ESCALA: 1/50

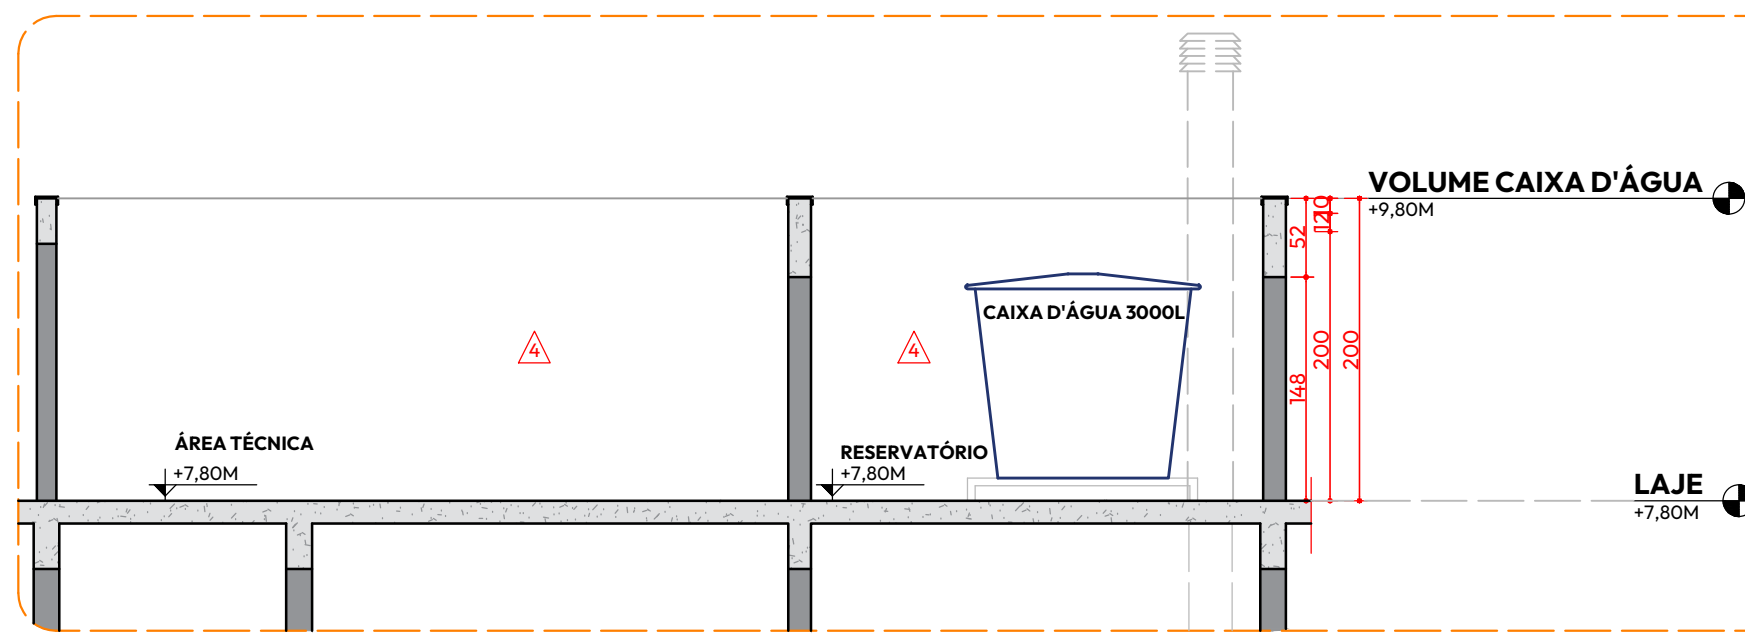


08 CORTE G/G - RESERVATÓRIO
ESCALA: 1/50



OBSERVAÇÕES DIVERSAS					
- CONSIDERAR NICHOS PARA BANHEIRA E ARMÁRIOS E AÉREOS.					
- CONSIDERAR NICHOS PARA LAVÁ-LOUÇAS E COZINHA E ESPAÇOS GOURMET.					
- CONSIDERAR REBAIXO DE 2 CM EM ÁREAS DE BOX DOS BANHEIROS.					
- CONSIDERAR VÊRGUA E CONTRAVÊRGUA EM TODAS AS ABERTURAS.					
- CONSIDERAR IMPERMEABILIZAÇÃO EM BANHEIROS, BALCÕES, LAJES APARENTES, SACADAS, FLOREIRAS E					
DEMÁS ÁREAS INDICADAS PELO RESPONSÁVEL PELA EXECUÇÃO.					
- CONSIDERAR RODAPÊ EMBUTIDO EM TODOS OS PAVIMENTOS.					
- CONSIDERAR INCLINAÇÃO DE NO MÍNIMO 2% E DRENOS EM ÁREAS DE LAJES IMPERMEABILIZADAS E TERRAÇOS.					
- DEIXAR ESPERA ELÉTRICA PARA ILUMINAÇÃO DE JARDIM.					
- QUALQUER DIFERENÇA DEVE SER COMPATIBILIZADA ANTES DA EXECUÇÃO.					
- OS MUIROS DE DIVISA DEVEM INICIAR A PARTIR DA FAIXA DE RECUE FRONTAL (3 METROS)					
- A CALÇADA DEVE SER EXECUTADA CONFORME PADRÃO ESTABELECIDO PELO CONDOMÍNIO.					
- A ALTURA MÁXIMA DO ARRIMO NÃO DEVE ULTRAPASSAR 2 METROS.					
- A TOPOGRAFIA DA CALÇADA DEVE PERMANECER NO PERFIL NATURAL.					
- TODAS AS CONDENAÇÕES DEVEM SER POSICIONADAS NA SACADA TÉCNICA JUNTO AO TELHADO. É					
ESTRITAMENTE PROIBIDO O POSICIONAMENTO EM FACHADAS.					
TABELA DE ACABAMENTOS DE PISO					
SÍMBOLOGIA	DESCRIÇÃO				
1	PORCELANATO				
2	MÁRMORE ESCOVADO				
3	MADERA ECOLÓGICA				
4	VINÍLICO COLADO				
5	CONCRETO BRUTO				
6	LAJE IMPERMEABILIZADA				
TABELA DE ACABAMENTOS DE PAREDE					
SÍMBOLOGIA	DESCRIÇÃO				
1	PORCELANATO				
2	MÁRMORE ESCOVADO				
3	PINTURA PROJETADA ESPECIAL				
4	PINTURA ACRILICA EXTERNA BRANCA A DEFINIR				
5	CONCRETO BRUTO				
6	PINTURA ACRILICA EXTERNA MARROM A DEFINIR				
7	PINTURA ACRILICA INTERNA A DEFINIR				
8	BRISÉ/ ANTEPARO EM SERRALHERIA				
TABELA DE ACABAMENTOS DE TETO					
SÍMBOLOGIA	DESCRIÇÃO				
1	MADERA ECOLÓGICA				
2	GESSO EM PINTURA ACRILICA A DEFINIR				
3	LAJE EM PINTURA ACRILICA A DEFINIR				
TABELA DE ESQUADRIAS - PORTAS					
SÍMBOLO	TAMANHO	VÃO	SISTEMA	ACABAMENTO	QUANTIDADE
P1	126X300CM	126X300CM	PIVOTANTE - PISO TETO	BEGE	01 UN
P2	80X300CM	87X300CM	GIRO - PISO TETO	BEGE	02 UN
P3	-	CONFERIR	PORTA + VÃO AMIGA	PRETO	01 UN
P4	80X300CM	87X300CM	GIRO - PISO TETO	ALUM. BEGE C/ FRISOS	03 UN
P5	313X300CM	313X300CM	GIRO - PISO TETO	ALUM. VIDRO PRETA	01 UN
P6	103X270CM	103X270CM	CORRER - PISO TETO	ALUM. VIDRO MARROM	01 UN
P7	80X270CM	87X270CM	CORRER - PISO TETO	A DEFINIR	03 UN
P8	80X270CM	87X270CM	GIRO	ALUM. MARROM C/ VENEZ.	02 UN
P9	80X270CM	87X270CM	GIRO	PVC BRANCO	02 UN
P10	100X270CM	100X270CM	CORRER	PVC BRANCO	02 UN
P11	390X280CM	390X280CM	PORTÃO ROLÔ	MADERA RIP. ECOLÓGICA	01 UN
P12	80X270CM	87X270CM	GIRO	PVC BRANCO	05 UN
TABELA DE ESQUADRIAS - JANELAS					
SÍMBOLO	TAMANHO	VÃO	SISTEMA	ACABAMENTO	QT.
J1	250X225/45CM	250X225/45CM	FIXA	ALUM. PRETO E VIDRO	01 UN
J2	280X270/30CM	280X270/30CM	CORRER 03 FOLHAS	ALUM. PRETO E VIDRO	01 UN
J3	120X270/30CM	120X270/30CM	MAXIMAR	ALUM. P. E VIDRO FOSCO	01 UN
J4	120X150/150CM	120X150/150CM	CORRER 02 FOLHAS	ALUM. PRETO E VIDRO	01 UN
J5	60X150/150CM	60X150/150CM	MAXIMAR	ALUM. P. E VIDRO FOSCO	01 UN
J6	214X213/52CM	214X213/52CM	CORRER 03 FOLHAS	ALUM. PRETO E VIDRO	01 UN
J7	300X213/52CM	300X213/52CM	CORRER 03 FOLHAS	ALUM. PRETO E VIDRO	01 UN
J8	333X213/52CM	333X213/52CM	CORRER 03 FOLHAS	ALUM. PRETO E VIDRO	01 UN
J9	150X213/52CM	150X213/52CM	CORRER 02 FOLHAS	ALUM. PRETO E VIDRO	01 UN
J10	330X213/52CM	330X213/52CM	CORRER 02 FOLHAS	ALUM. PRETO E VIDRO	01 UN
J11	100X213/52CM	100X213/52CM	CORRER 03 FOLHAS	ALUM. P. E VIDRO FOSCO	02 UN
J12	87X213/52CM	87X213/52CM	CORRER 03 FOLHAS	ALUM. P. E VIDRO FOSCO	02 UN
J13	200X213/52CM	200X213/52CM	CORRER 03 FOLHAS	ALUM. P. E VIDRO FOSCO	01 UN
J14	400X213/52CM	400X213/52CM	CORRER 03 FOLHAS	ALUM. PRETO E VIDRO	01 UN
J15	414X213/52CM	414X213/52CM	FIXA - 01 FOLHA	ALUM. PRETO E VIDRO	01 UN
J16	105X213/52CM	105X213/52CM	FIXA - 04 FOLHAS	ALUM. PRETO E VIDRO	01 UN
J17	220X80/130CM	220X80/130CM	CORRER 02 FOLHAS	ALUM. PRETO E VIDRO	01 UN
REVISÕES:					
REVISÃO	DATA	DESCRIÇÃO	DESENHO		
R02	29/08/25	CORREÇÃO DO QUADRO DE ESTATÍSTICAS	JOSE		
R03	29/08/25	CORREÇÃO DO QUADRO DE ESTATÍSTICAS	JOSE		
R04	04/02/26	COMPATIBILIZAÇÃO DO PROJETO DE INTERIORES	JOSE		
ESTATÍSTICAS:					
ÁREA DO TERRENO	418,16M²	TAXA DE OCUPAÇÃO (177,24M²):	42,39%		
ÁREA A CONSTRUIR TERREO	177,24M²	COEFICIENTE DE APROVEITAMENTO:	1,0153		
ÁREA A CONSTRUIR SUPERIOR	122,24M²	TAXA DE PERMEABILIDADE:	38,94%		
ÁREA A CONSTRUIR SUBSOLO	120,08M²	ESCADARIA ENTRADA (CONCRETO)	11,88M²		
ÁREA TOTAL A CONSTRUIR	424,58M²	ÁREA DECK	6,94M²		
ÁREA PERMEÁVEL	162,85M²	ÁREA PISCINA	18,09M²		
SENDO:		ÁREA VARANDA/ CALÇADAS/ BORDAS	26,99M²		
GRAMA	113,15M²	ÁREA MURETAS	2,83M²		
DRENANTE (85X):	58,48M²	ÁREA FLOREIRAS NÃO PERMEÁVEIS	4,57M²		
ORGÃOS PÚBLICOS:					
PROJETO ARQUITETÔNICO RESIDENCIAL					
ARQUITETO:	GEOVANI CEZAR FELTRIN	CAU:	A130445-3		
EXECUÇÃO:	MACIEL COSTA DA SILVA	CPF:	064.664.969-88		
PROPRIETÁRIO:	MACIEL E FERNANDO				
LOCAL:	CONDOMÍNIO TERRAS ALPHA CASCAVEL, QUADRA 001, UNIDADE 16	ESCALA:	INDICADA		
CONTEÚDO:	PAV. TERREO/ SUPERIOR/ DET. RESERVATÓRIO	FOLHA:	EXE.02		
		DESENHO:	JOSE		
		DATA:	09/04/25		
			EXE.05		
A APROVAÇÃO DO PRESENTE PROJETO PELA PREFEITURA NÃO RECONHECE A PROPRIEDADE DO IMÓVEL					

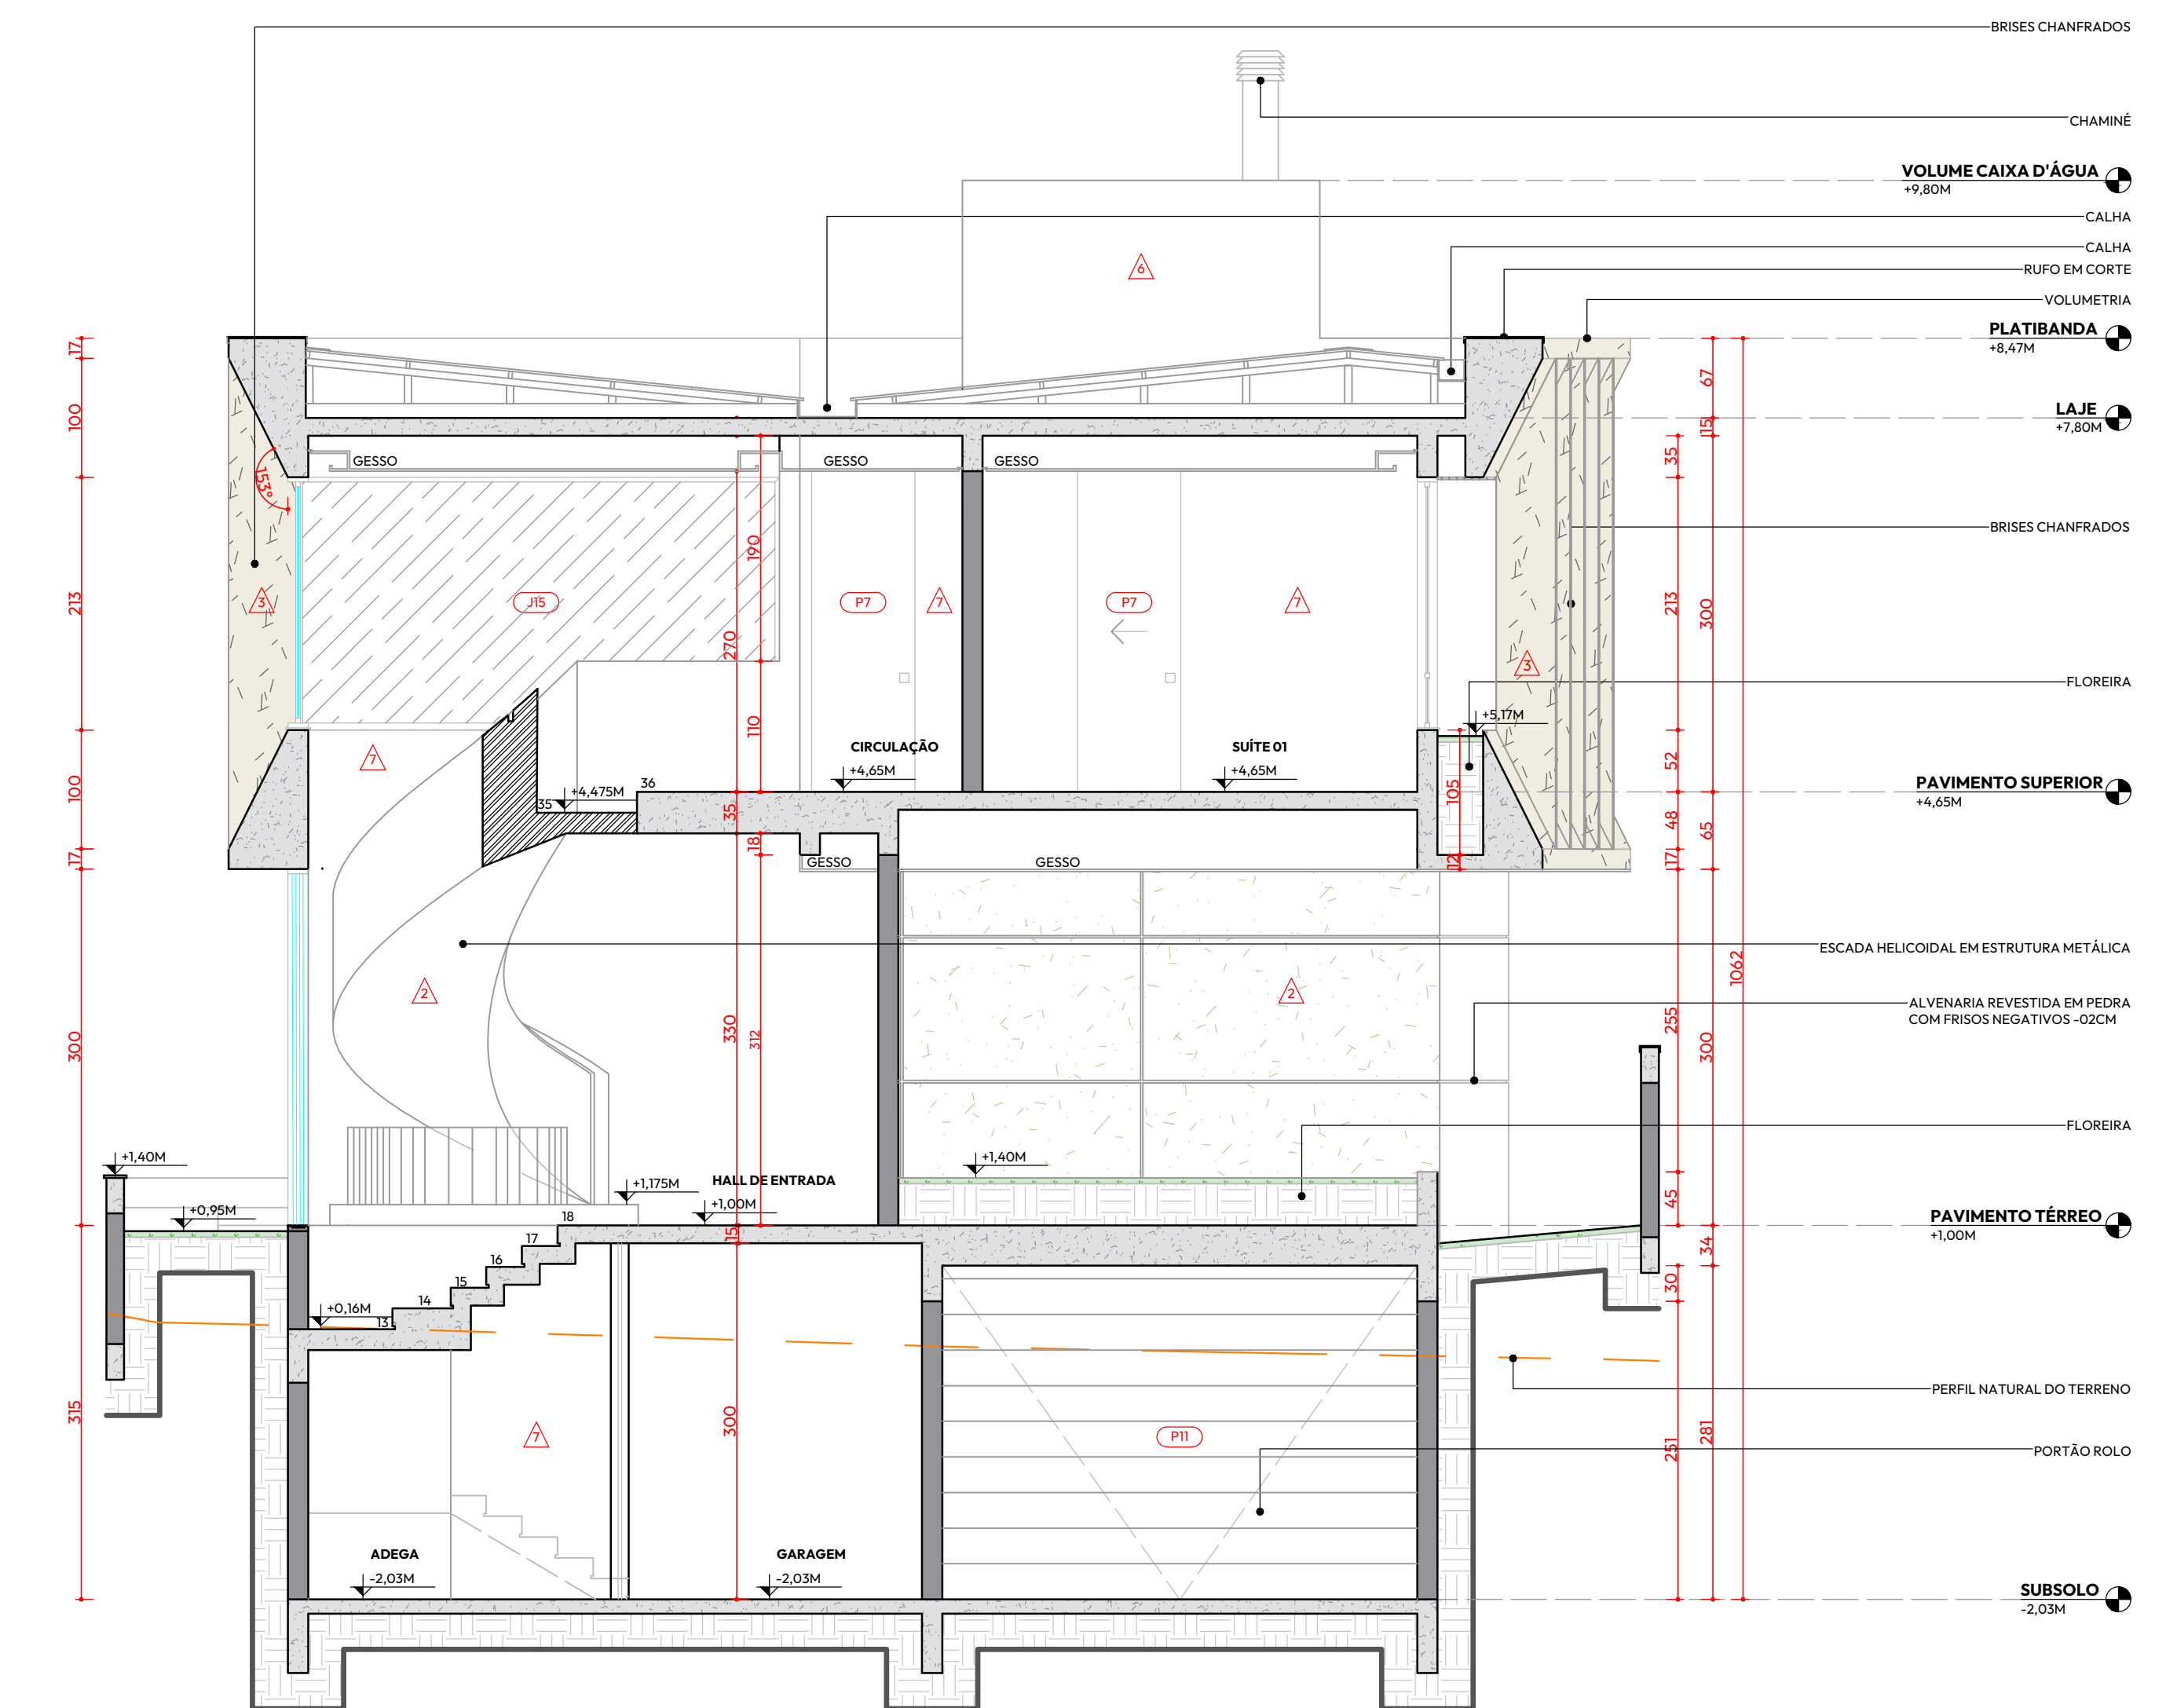

07 CORTE A/A
ESCALA: 1/50

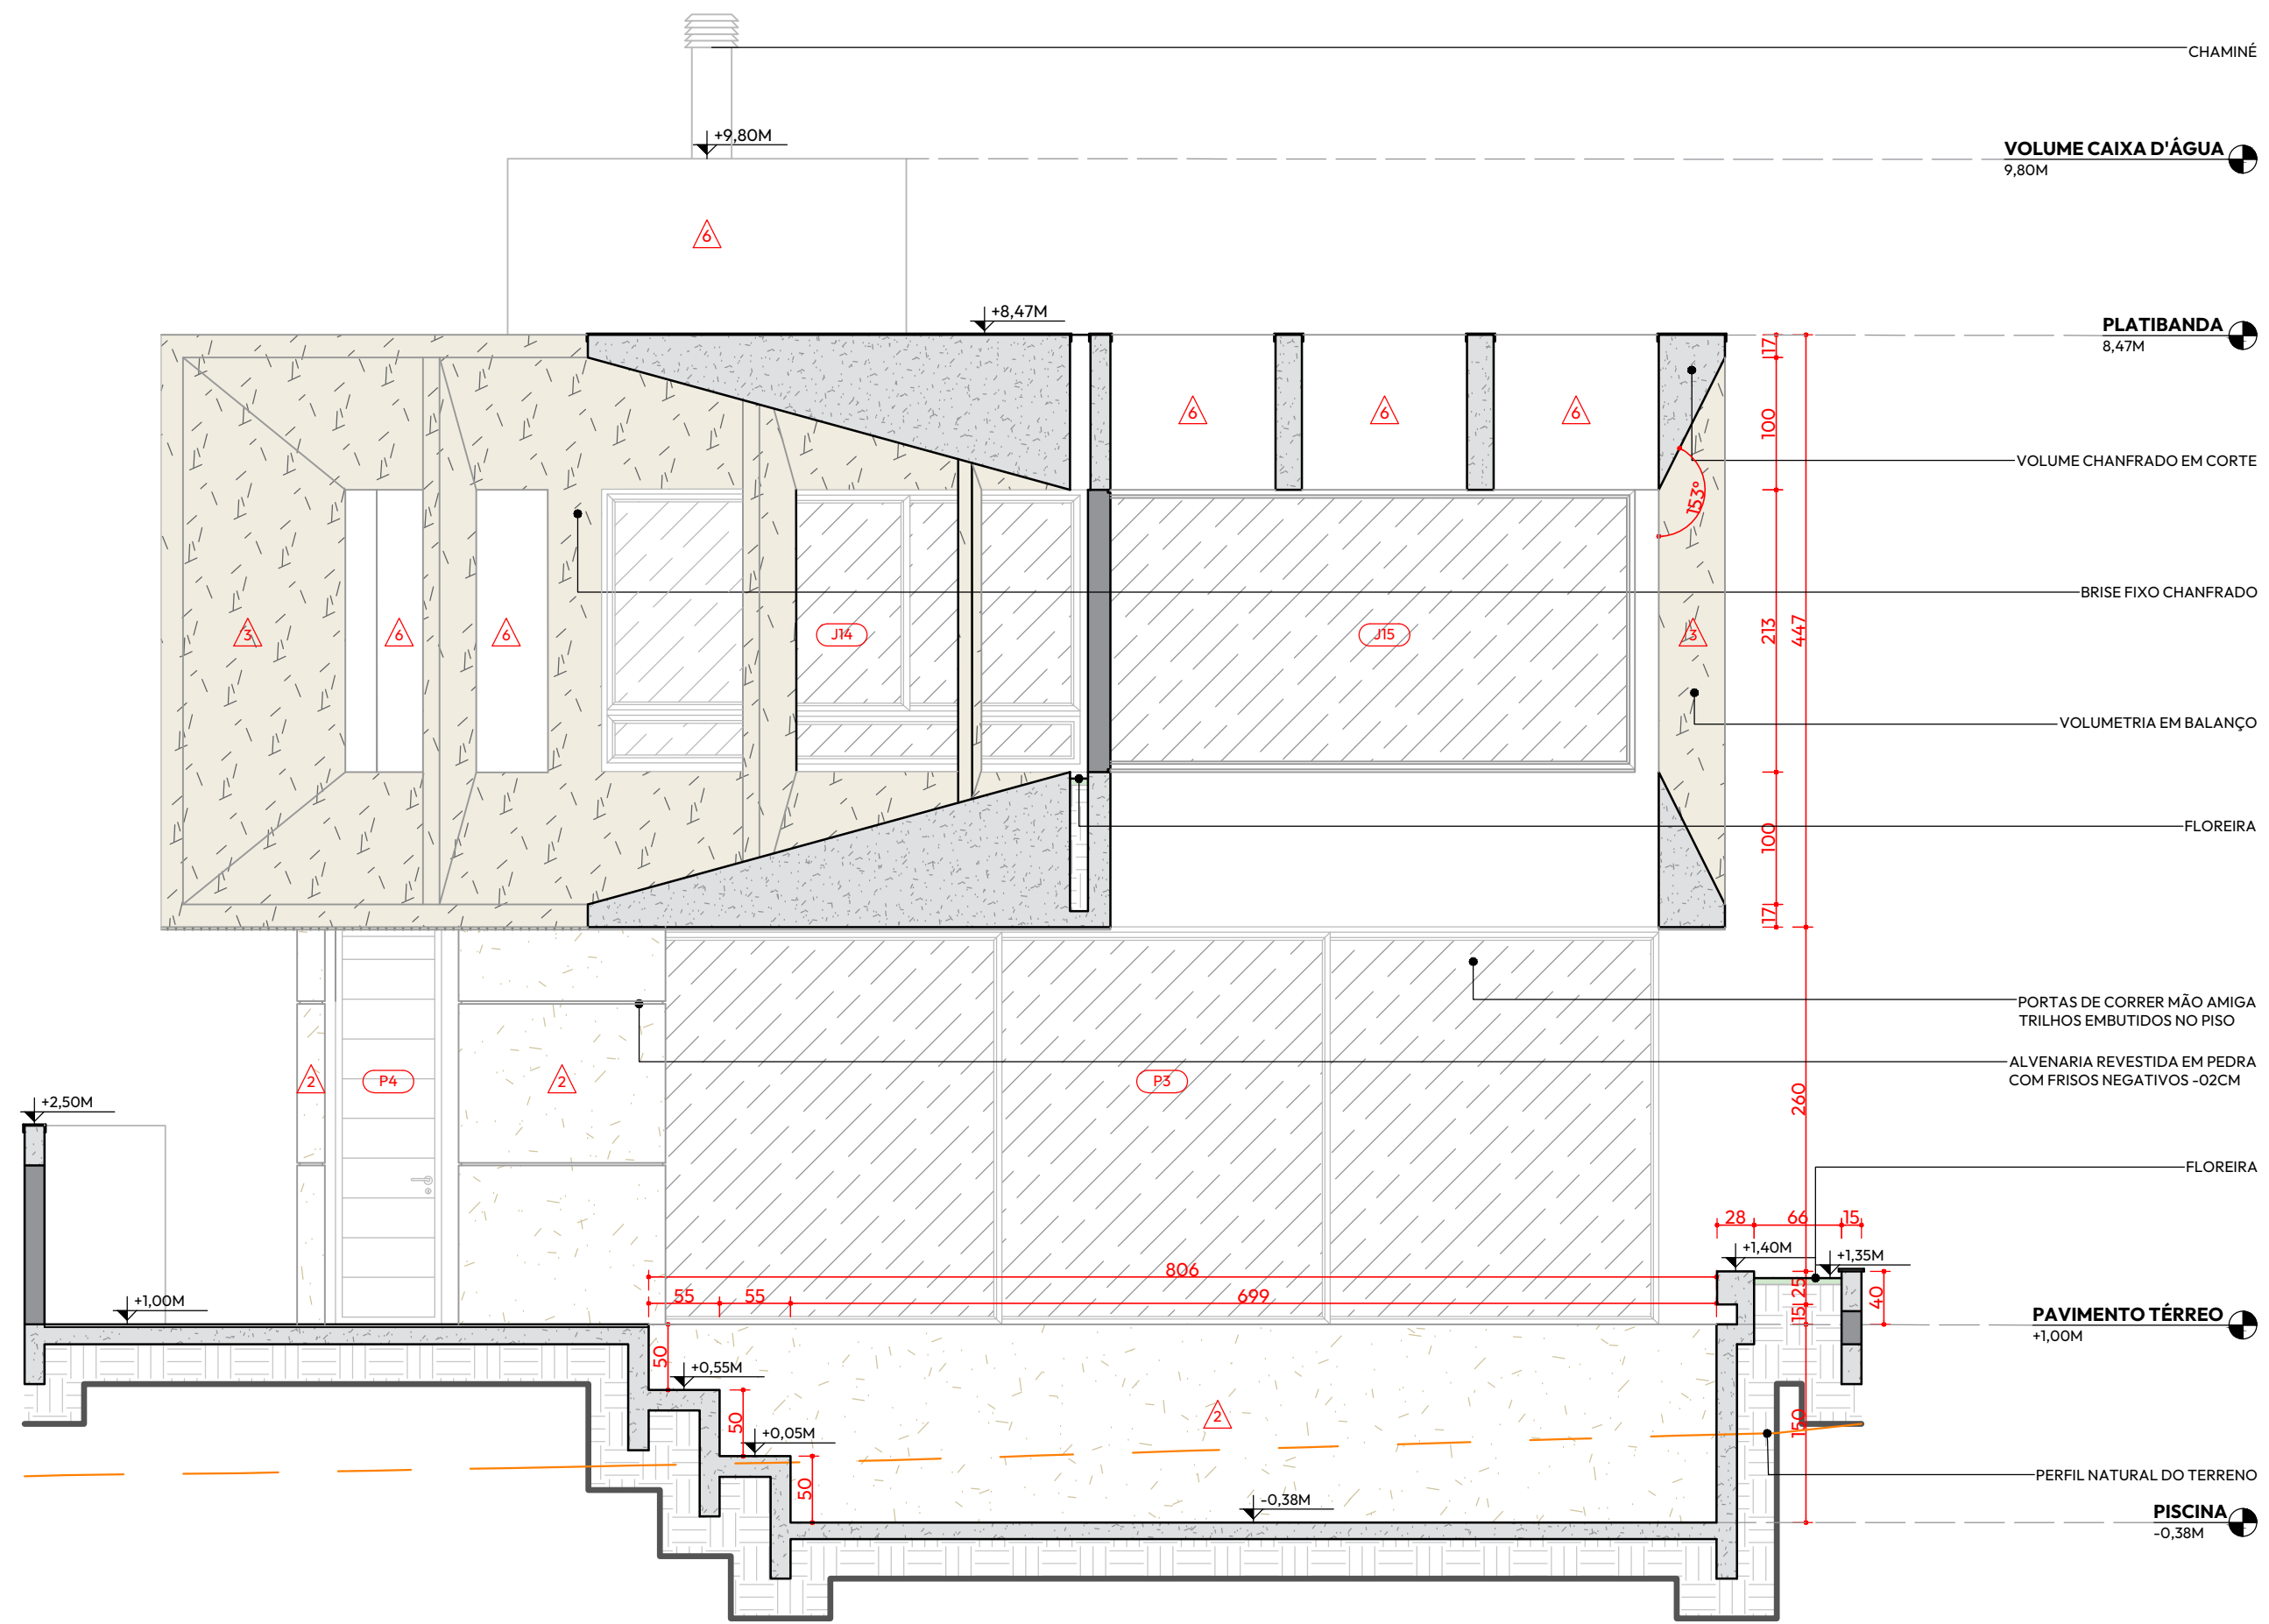

09 CORTE C/C
ESCALA: 1/50

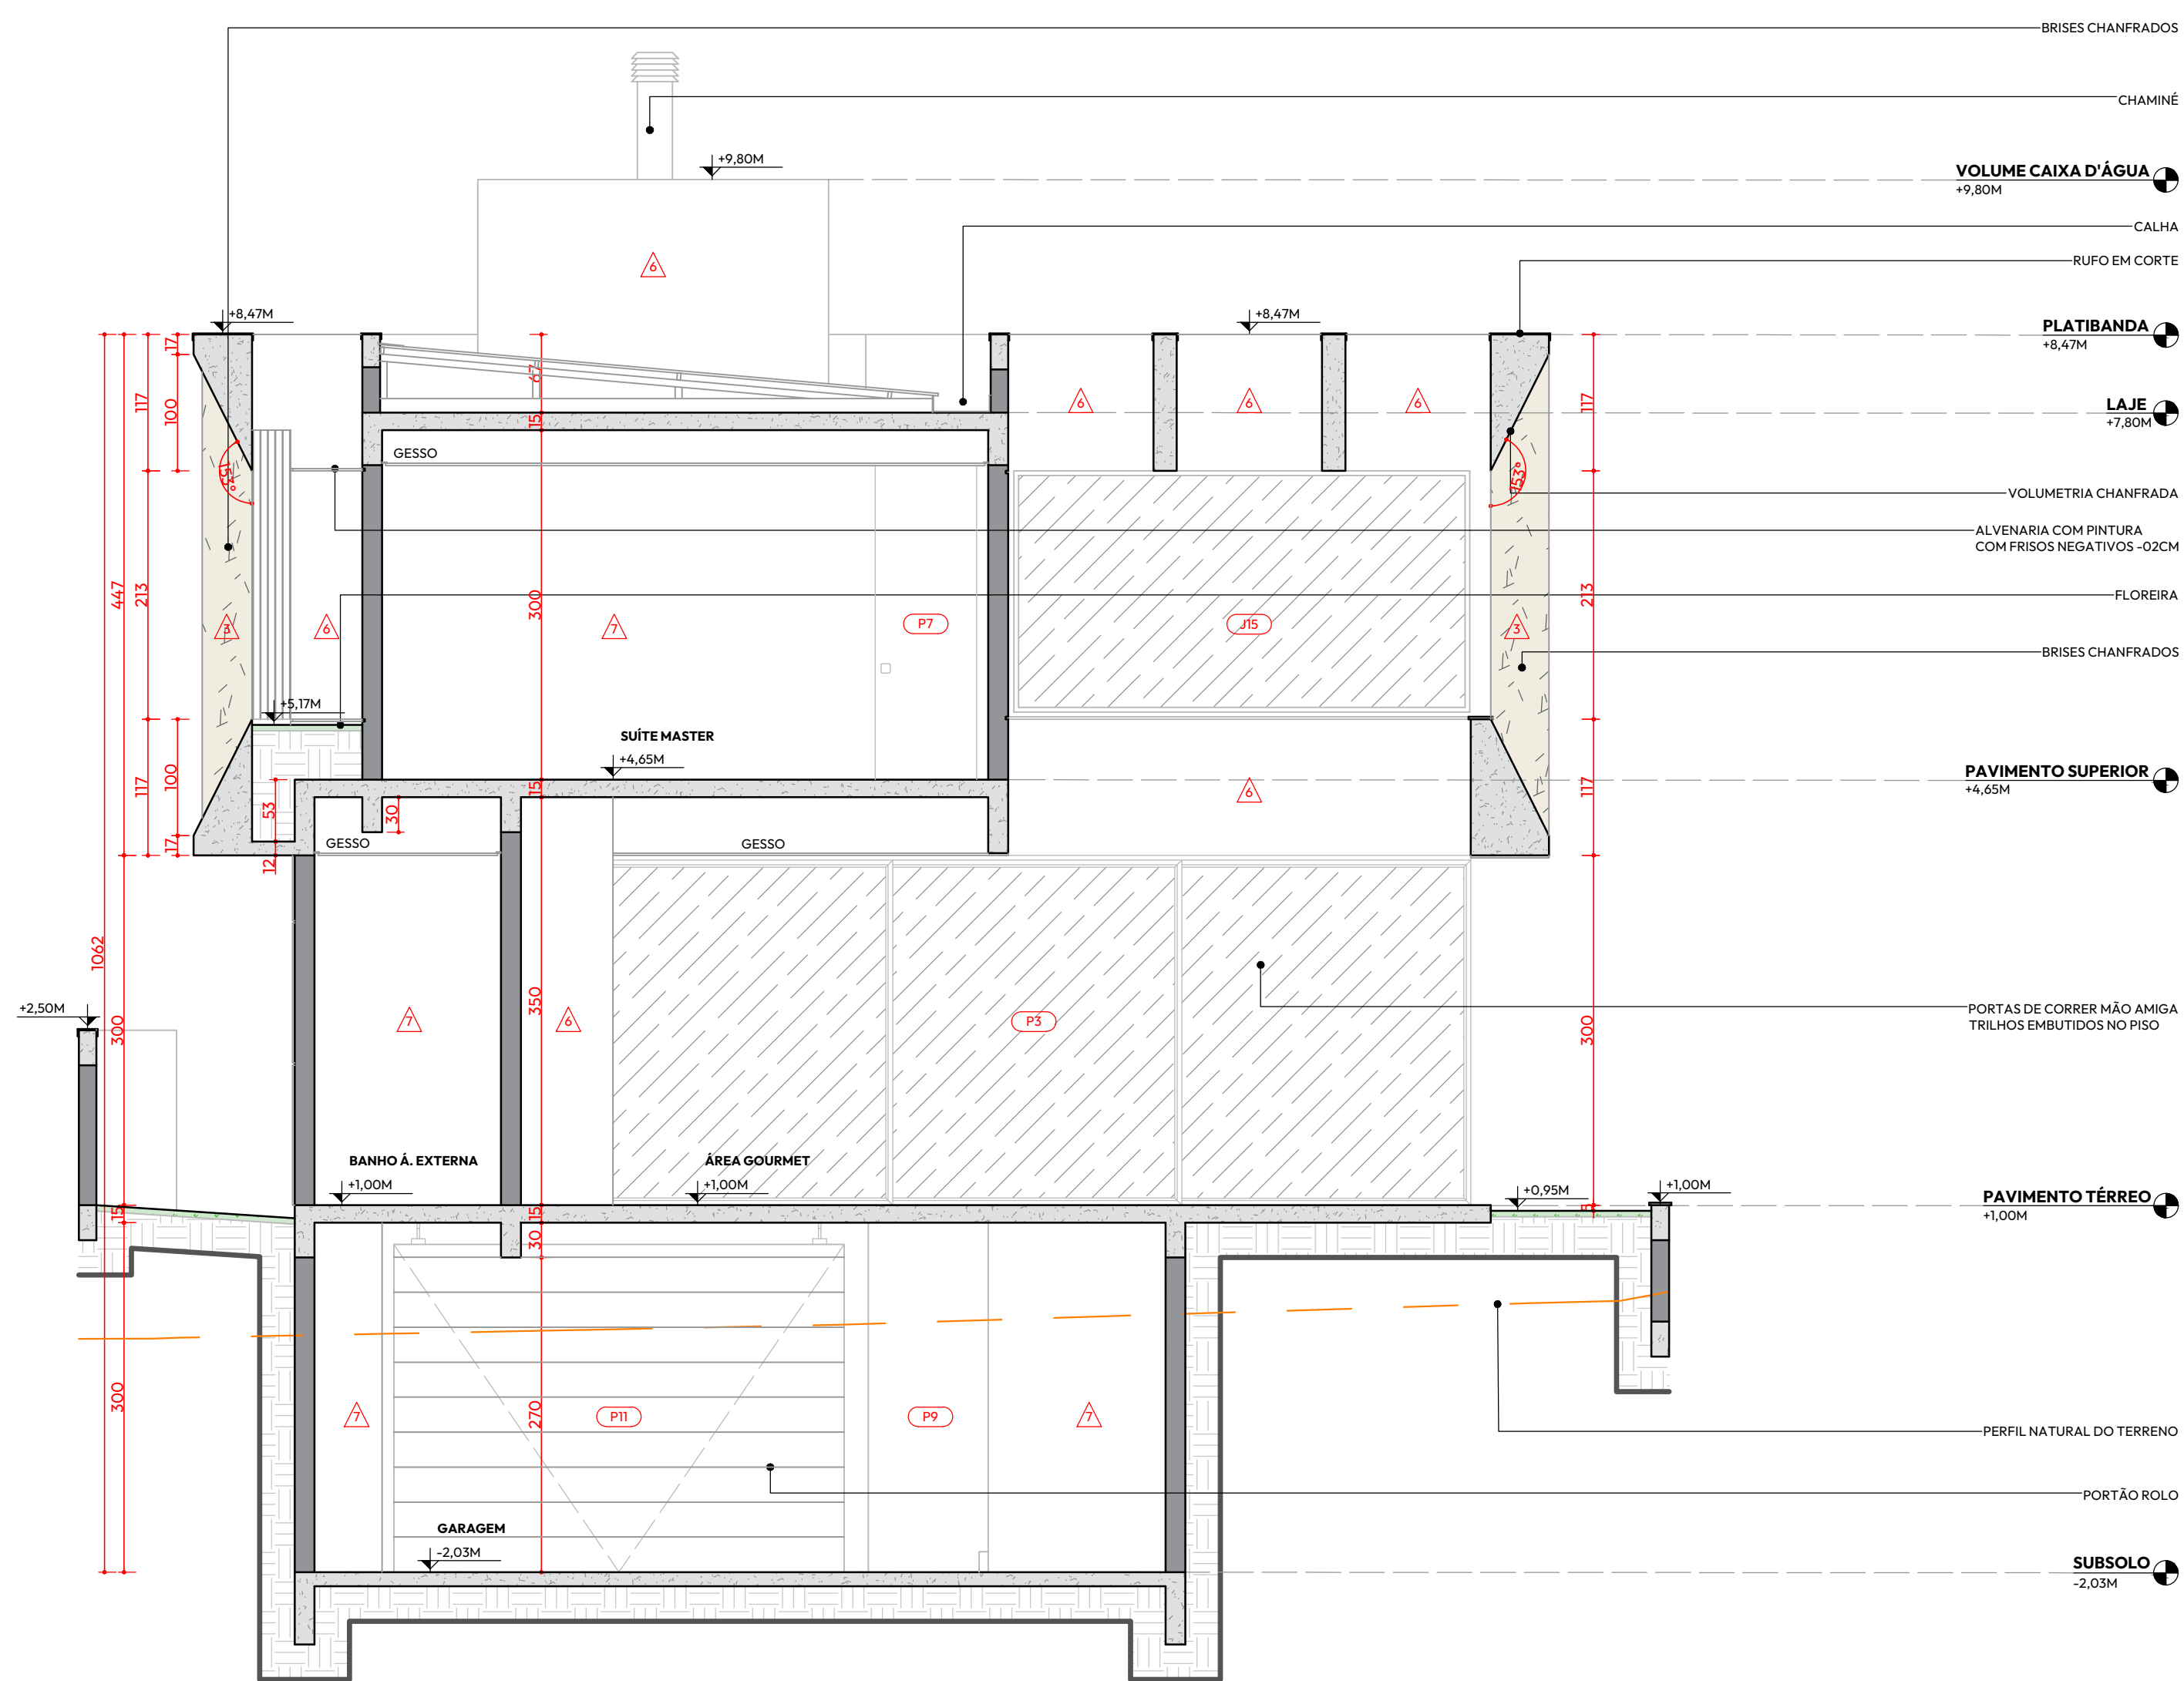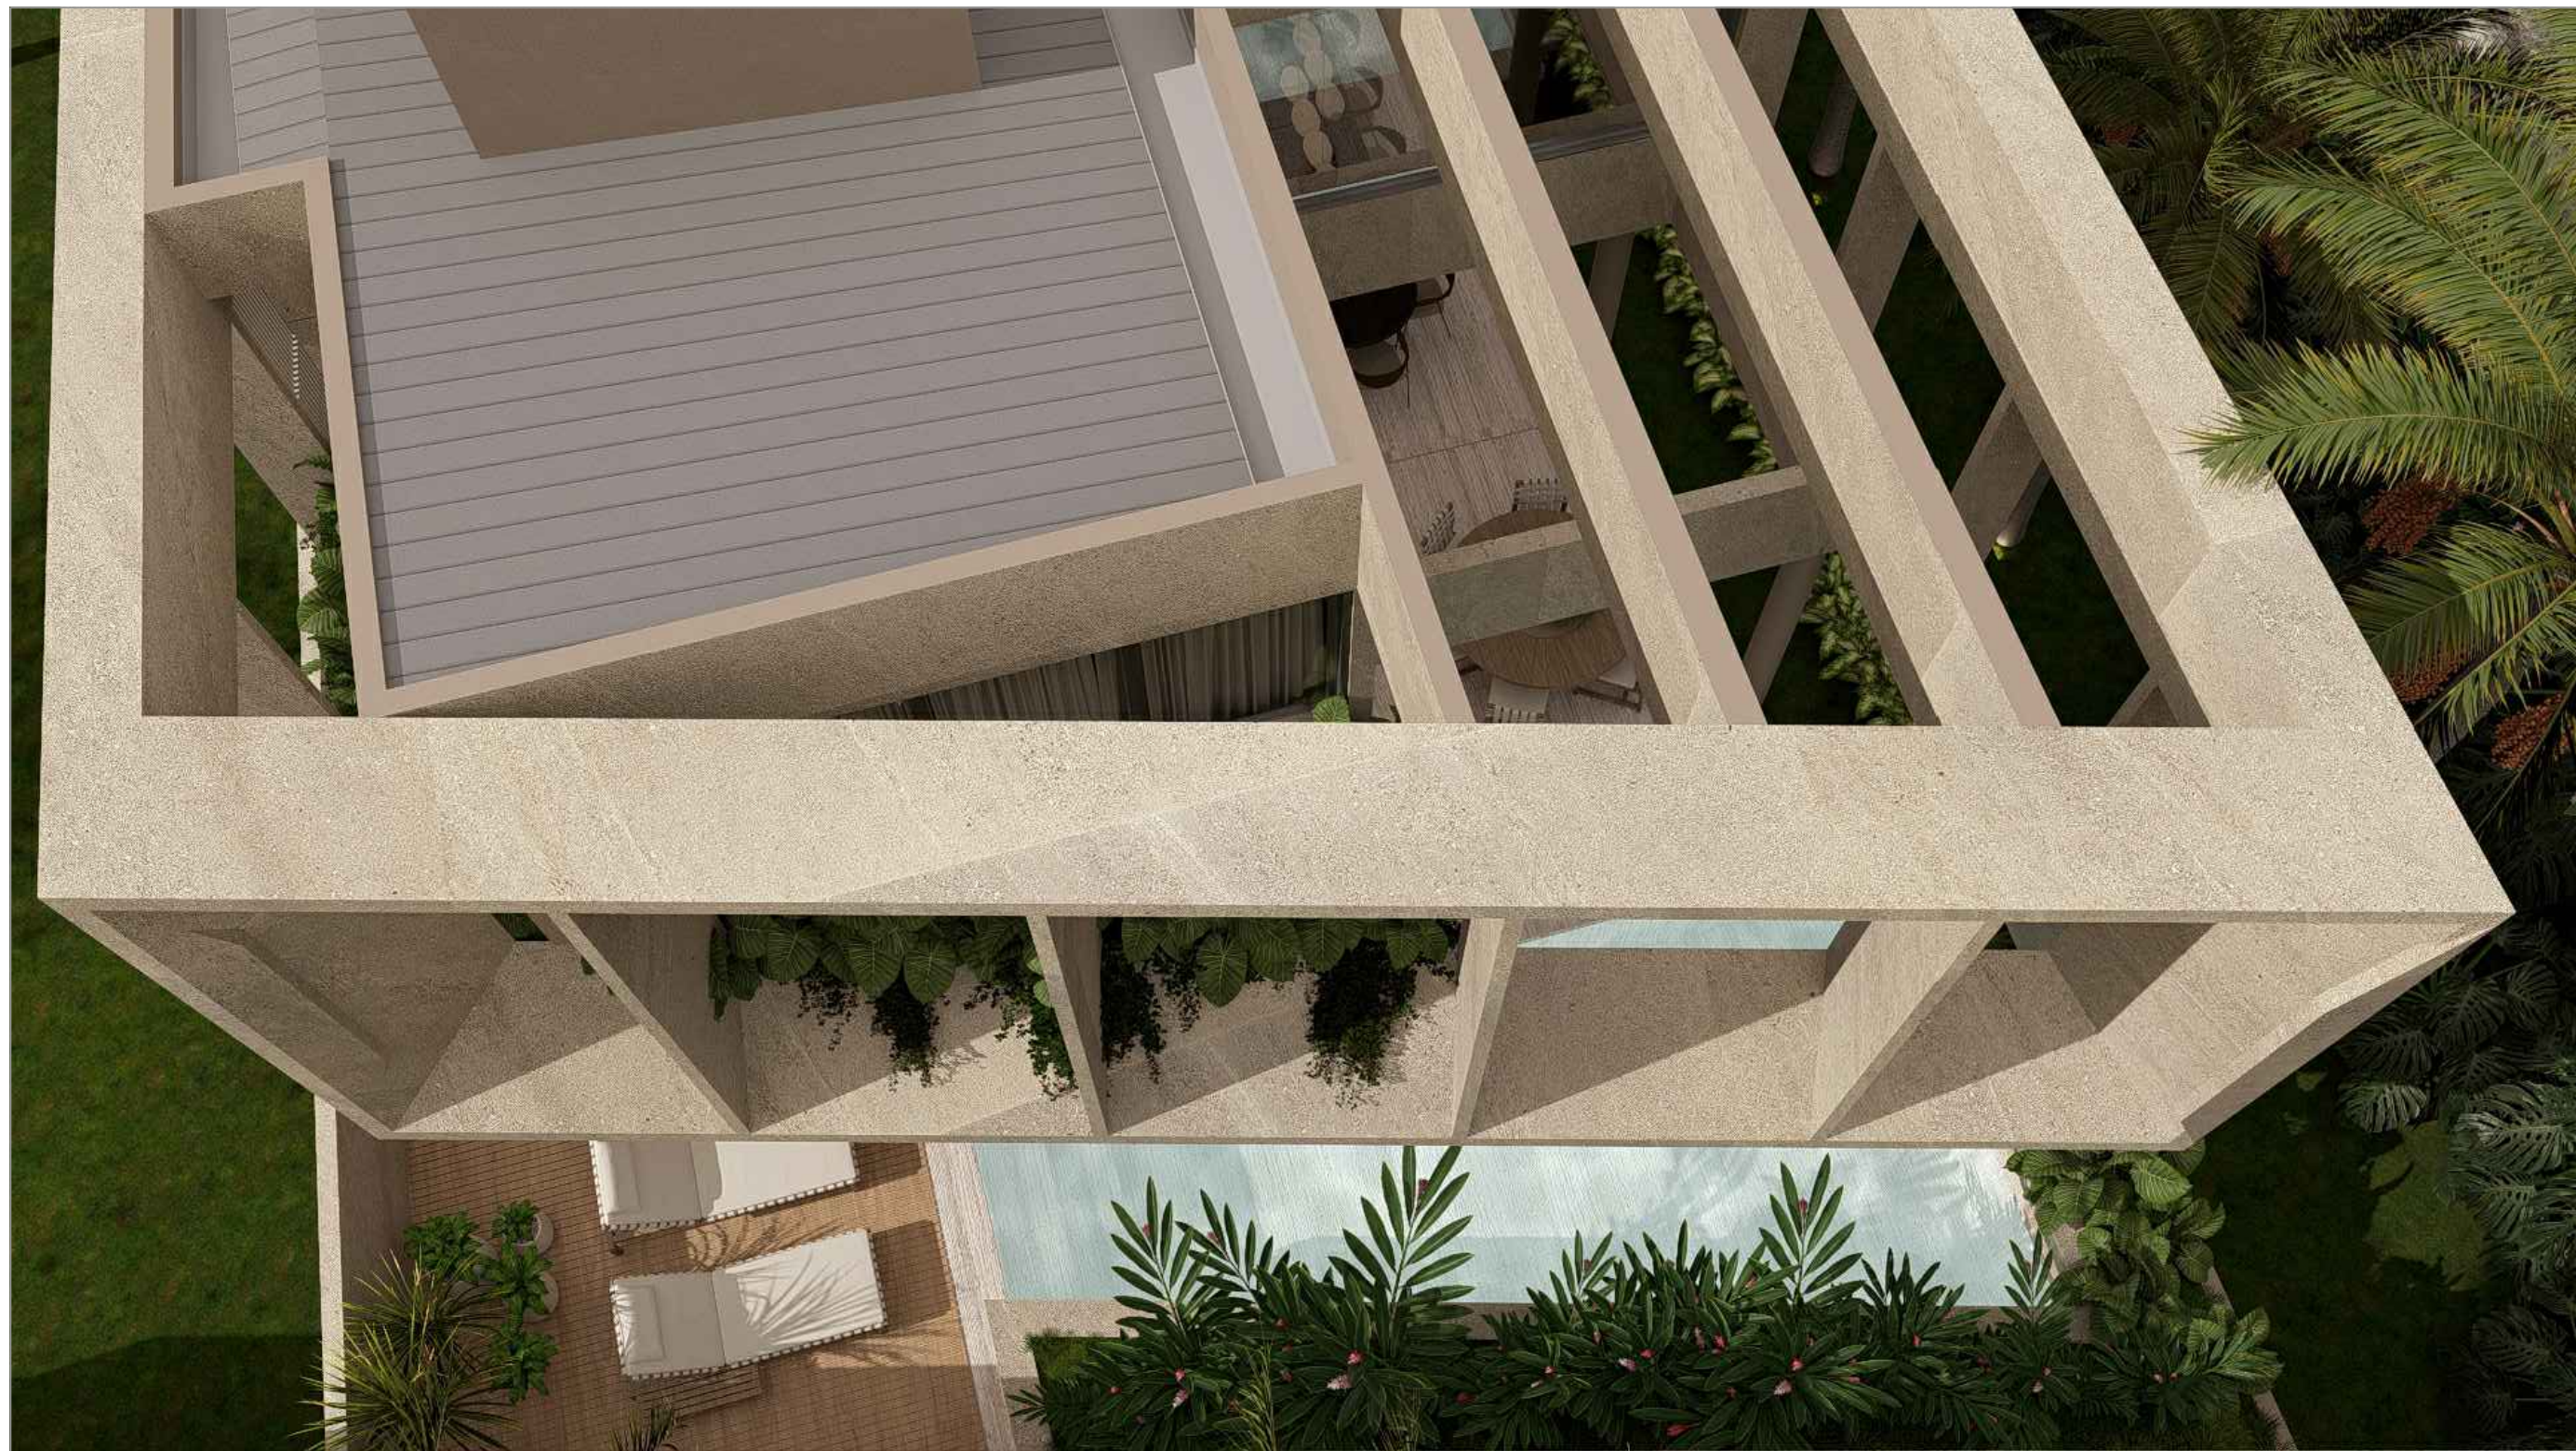

08 CORTE B/B
ESCALA: 1/50



- OBSERVAÇÕES DIVERSAS
- CONSIDERAR NICHOS PARA BANHEIRA E ARMÁRIOS E AÉREOS.
 - CONSIDERAR NICHOS PARA LAVAS-LOUÇAS E COZINHAS E ESPAÇOS GOURMETS.
 - CONSIDERAR REBAIXO DE 2 CM EM ÁREAS DE BOX DOS BANHEIROS.
 - CONSIDERAR VENTIL. CONTRAVENTIDA EM TODAS AS ABERTURAS.
 - CONSIDERAR IMPERMEABILIZAÇÃO EM BANHEIROS, BALCÕES, LAJES, APARTELES, SACADAS, FLOREIRAS E DEMAS ÁREAS INDICADAS PELO RESPONSÁVEL PELA EXECUÇÃO.
 - CONSIDERAR RODAPÊ EMBUTIDO EM TODOS OS PAVIMENTOS.
 - CONSIDERAR INCLINAÇÃO DE NO MÍNIMO 2% E DRENOS EM ÁREAS DE LAJES IMPERMEABILIZADAS E TERRAÇOS.
 - DEIXAR ESPERA ELÉTRICA PARA ILUMINAÇÃO DE JARDIM.
 - QUAL QUER DIVERGÊNCIA DEVE SER COMPATIBILIZADA ANTES DA EXECUÇÃO.
 - A TOPOGRAFIA DA CALÇADA DEVE PERMANECER NO PERFIL NATURAL.
 - OS MUIROS DE DIVISA DEVEM INICIAR A PARTIR DA FAIXA DE RECUE FRONTAL (3 METROS).
 - A ALTURA MÁXIMA DOS MUIROS EM RELAÇÃO AO PERFIL MODIFICADO DO TERRENO OU DO ARRIMO NÃO DEVE ULTRAPASSAR 2 METROS.
 - A ALTURA MÁXIMA DO ARRIMO NÃO DEVE ULTRAPASSAR 2 METROS.
 - A TOPOGRAFIA DA CALÇADA DEVE PERMANECER NO PERFIL NATURAL.
 - A CALÇADA DEVE SER EXECUTADA CONFORME PADRÃO ESTABELECIDO PELO CONDOMÍNIO.
 - TODAS AS CONDENSADORAS DEVEM SER POSICIONADAS NA SACADA TÉCNICA JUNTO AO TELHADO. É ESTRITAMENTE PROIBIDO O POSICIONAMENTO EM FACHADAS.

TABELA DE ACABAMENTOS DE PISO	
SÍMBOLOGIA	DESCRIÇÃO
1	PORCELANATO
2	MÁRMORE ESCOVADO
3	MADERA ECOLÓGICA
4	VINÍLICO COLADO
5	CONCRETO BRUTO
6	LAJE IMPERMEABILIZADA

TABELA DE ACABAMENTOS DE PAREDE	
SÍMBOLOGIA	DESCRIÇÃO
1	PORCELANATO
2	MÁRMORE ESCOVADO
3	PINTURA PROJETADA ESPECIAL
4	PINTURA ACRILICA EXTERNA BRANCA A DEFINIR
5	CONCRETO BRUTO
6	PINTURA ACRILICA EXTERNA MARROM A DEFINIR
7	PINTURA ACRILICA INTERNA A DEFINIR
8	BRISÉ/ ANTEPARO EM SERRALHERIA

TABELA DE ACABAMENTOS DE TETO	
SÍMBOLOGIA	DESCRIÇÃO
1	MADERA ECOLÓGICA
2	GESSO EM PINTURA ACRILICA A DEFINIR
3	LAJE EM PINTURA ACRILICA A DEFINIR

TABELA DE ESQUADRIAS - PORTAS					
SÍMBOLO	TAMANHO	VÃO	SISTEMA	ACABAMENTO	QUANTIDADE
P1	126X300CM	126X300CM	PIVOTANTE - PISO TETO	BEGE	01 UN
P2	80X300CM	87X300CM	GIRO - PISO TETO	BEGE	02 UN
P3	-	CONFERIR	PORTA V. MÃO ANGA TRILHO EMBUTIDO PISO	PRETO	01 UN
P4	80X300CM	87X300CM	GIRO - PISO TETO	ALUM. BEGE C/ FRISOS	03 UN
P5	313X300CM	313X300CM	GIRO - PISO TETO	ALUM. VIDRO PRETA	01 UN
P6	103X270CM	103X270CM	CORRER - PISO TETO	ALUM. VIDRO MARROM	01 UN
P7	80X270CM	87X270CM	CORRER - PISO TETO	A DEFINIR	03 UN
P8	80X100CM	87X100CM	GIRO	ALUM. MARROM C/ VENEZ.	02 UN
P9	80X270CM	87X270CM	GIRO	PVC BRANCO	02 UN
P10	120X270CM	120X270CM	CORRER	PVC BRANCO	02 UN
P11	390X281CM	390X281CM	PORTÃO GIRO	MADERA RIP. ECOLÓGICA	01 UN
P12	80X270CM	87X270CM	GIRO	PVC BRANCO	05 UN

TABELA DE ESQUADRIAS - JANELAS				
SÍMBOLO	TAMANHO	VÃO	SISTEMA	ACABAMENTO
J1	250X255/45CM	250X255/45CM	FIXA	ALUM. PRETO E VIDRO
J2	280X270/30CM	280X270/30CM	CORRER 03 FOLHAS	ALUM. PRETO E VIDRO
J3	120X270/30CM	120X270/30CM	MAXIM AR	ALUM. P. E VIDRO FOSCO
J4	120X150/150CM	120X150/150CM	CORRER 02 FOLHAS	ALUM. PRETO E VIDRO
J5	60X150/150CM	60X150/150CM	MAXIM AR	ALUM. P. E VIDRO FOSCO
J6	214X213/52CM	214X213/52CM	CORRER 03 FOLHAS	ALUM. PRETO E VIDRO
J7	300X213/52CM	300X213/52CM	CORRER 03 FOLHAS	ALUM. PRETO E VIDRO
J8	333X213/52CM	333X213/52CM	CORRER 03 FOLHAS	ALUM. PRETO E VIDRO
J9	150X120/150CM	150X120/150CM	CORRER 02 FOLHAS	ALUM. PRETO E VIDRO
J10	330X213/52CM	330X213/52CM	CORRER 03 FOLHAS	ALUM. PRETO E VIDRO
J11	100X213/52CM	100X213/52CM	CORRER 03 FOLHAS	ALUM. P. E VIDRO FOSCO
J12	87X213/52CM	87X213/52CM	CORRER 03 FOLHAS	ALUM. P. E VIDRO FOSCO
J13	200X213/52CM	200X213/52CM	CORRER 03 FOLHAS	ALUM. P. E VIDRO FOSCO
J14	400X213/52CM	400X213/52CM	CORRER 03 FOLHAS	ALUM. PRETO E VIDRO
J15	414X413/365CM	414X413/365CM	FIXA - 01 FOLHA	ALUM. PRETO E VIDRO
J16	1055X213/52CM	1055X213/52CM	FIXA - 04 FOLHAS	ALUM. PRETO E VIDRO
J17	220X80/130CM	220X80/130CM	CORRER 02 FOLHAS	ALUM. PRETO E VIDRO

REVISÕES:

REVISÃO	DATA	DESCRIÇÃO	DESENHO
R02	29/08/25	CORREÇÃO DO QUADRO DE ESTATÍSTICAS	JOSE
R03	29/08/25	CORREÇÃO DO QUADRO DE ESTATÍSTICAS	JOSE
R04	04/02/26	COMPATIBILIZAÇÃO DO PROJETO DE INTERIORES	JOSE

ESTATÍSTICAS:

ÁREA DO TERRENO	418,16M²	TAXA DE OCUPAÇÃO (177,24M²):	42,39%
ÁREA A CONSTRUIR TERREO	177,24M²	COEFICIENTE DE APROVEITAMENTO:	1,0153
ÁREA A CONSTRUIR SUPERIOR	122,20M²	TAXA DE PERMEABILIDADE:	38,94%
ÁREA A CONSTRUIR SUBSOLO	120,08M²	ESCADARIA ENTRADA (CONCRETO)	6,94M²
ÁREA TOTAL A CONSTRUIR	424,58M²	ÁREA DECK	11,88M²
ÁREA PERMEÁVEL	162,85M²	ÁREA PISCINA	38,09M²
SENDO:		ÁREA VASARIADA/ CALÇADAS/ BORDAS	26,99M²
GRAMA:	113,15M²	ÁREA MURETAS	2,83M²
DRENANTE (80X)	58,48M²	ÁREA FLOREIRAS NÃO PERMEÁVEIS	4,57M²

ÓRGÃOS PÚBLICOS:

PROJETO ARQUITETÔNICO RESIDENCIAL


ARQUITETO: GEOVANI CEZAR FELTRIN CAU: A130445-3

EXECUÇÃO: MACIEL COSTA DA SILVA CPF: 064.664.969-88


PROPRIETÁRIO: MACIEL E FERNANDO

LOCAL:	CONDOMÍNIO TERRAS ALPHA CASCAVEL, QUADRA 001, UNIDADE 16	ESCALA:	INDICADA	FOLHA:	EXE.03
CONTEÚDO:	CORTES A B C	DESENHO:	JOSE	DATA:	09/06/25
					EXE.05

A APROVAÇÃO DO PRESENTE PROJETO PELA PREFEITURA NÃO RECONHECE A PROPRIEDADE DO IMÓVEL

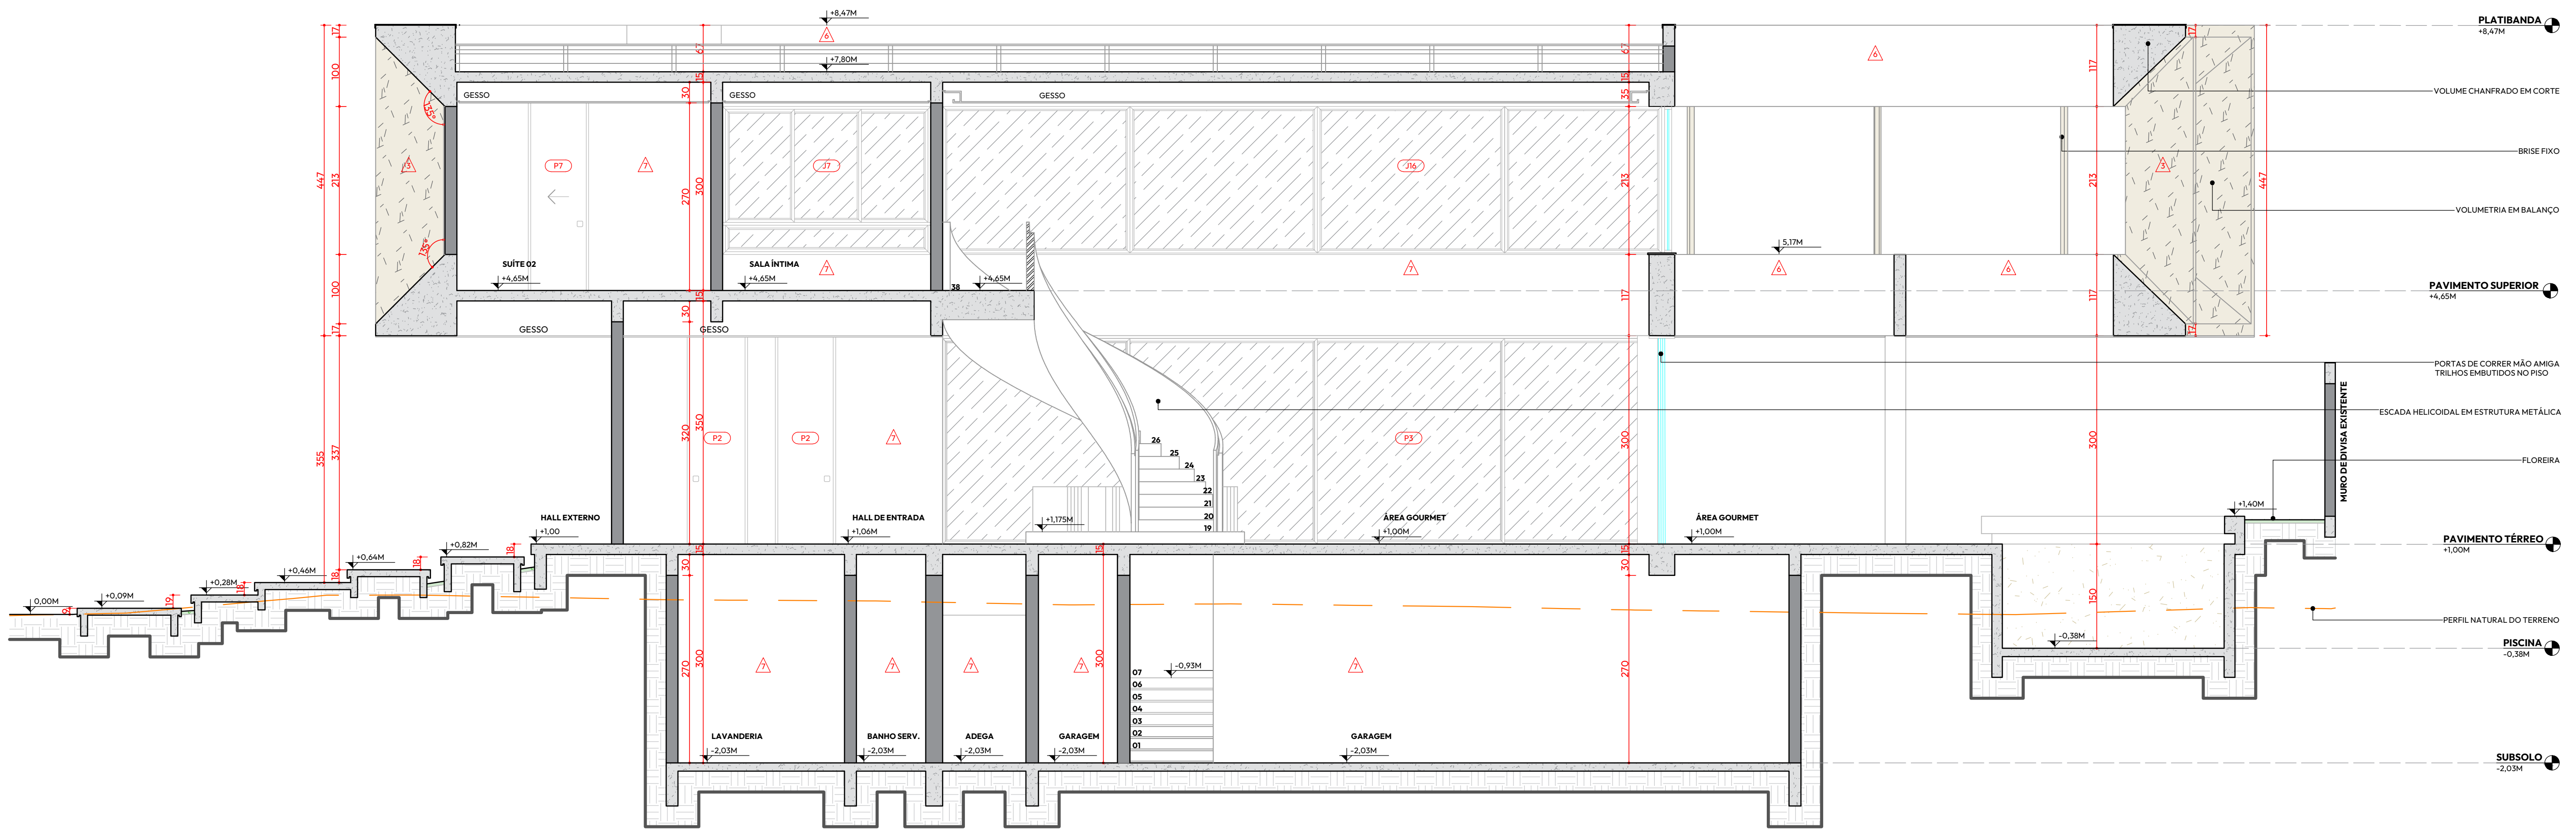

10 CORTED/D
ESCALA: 1/50

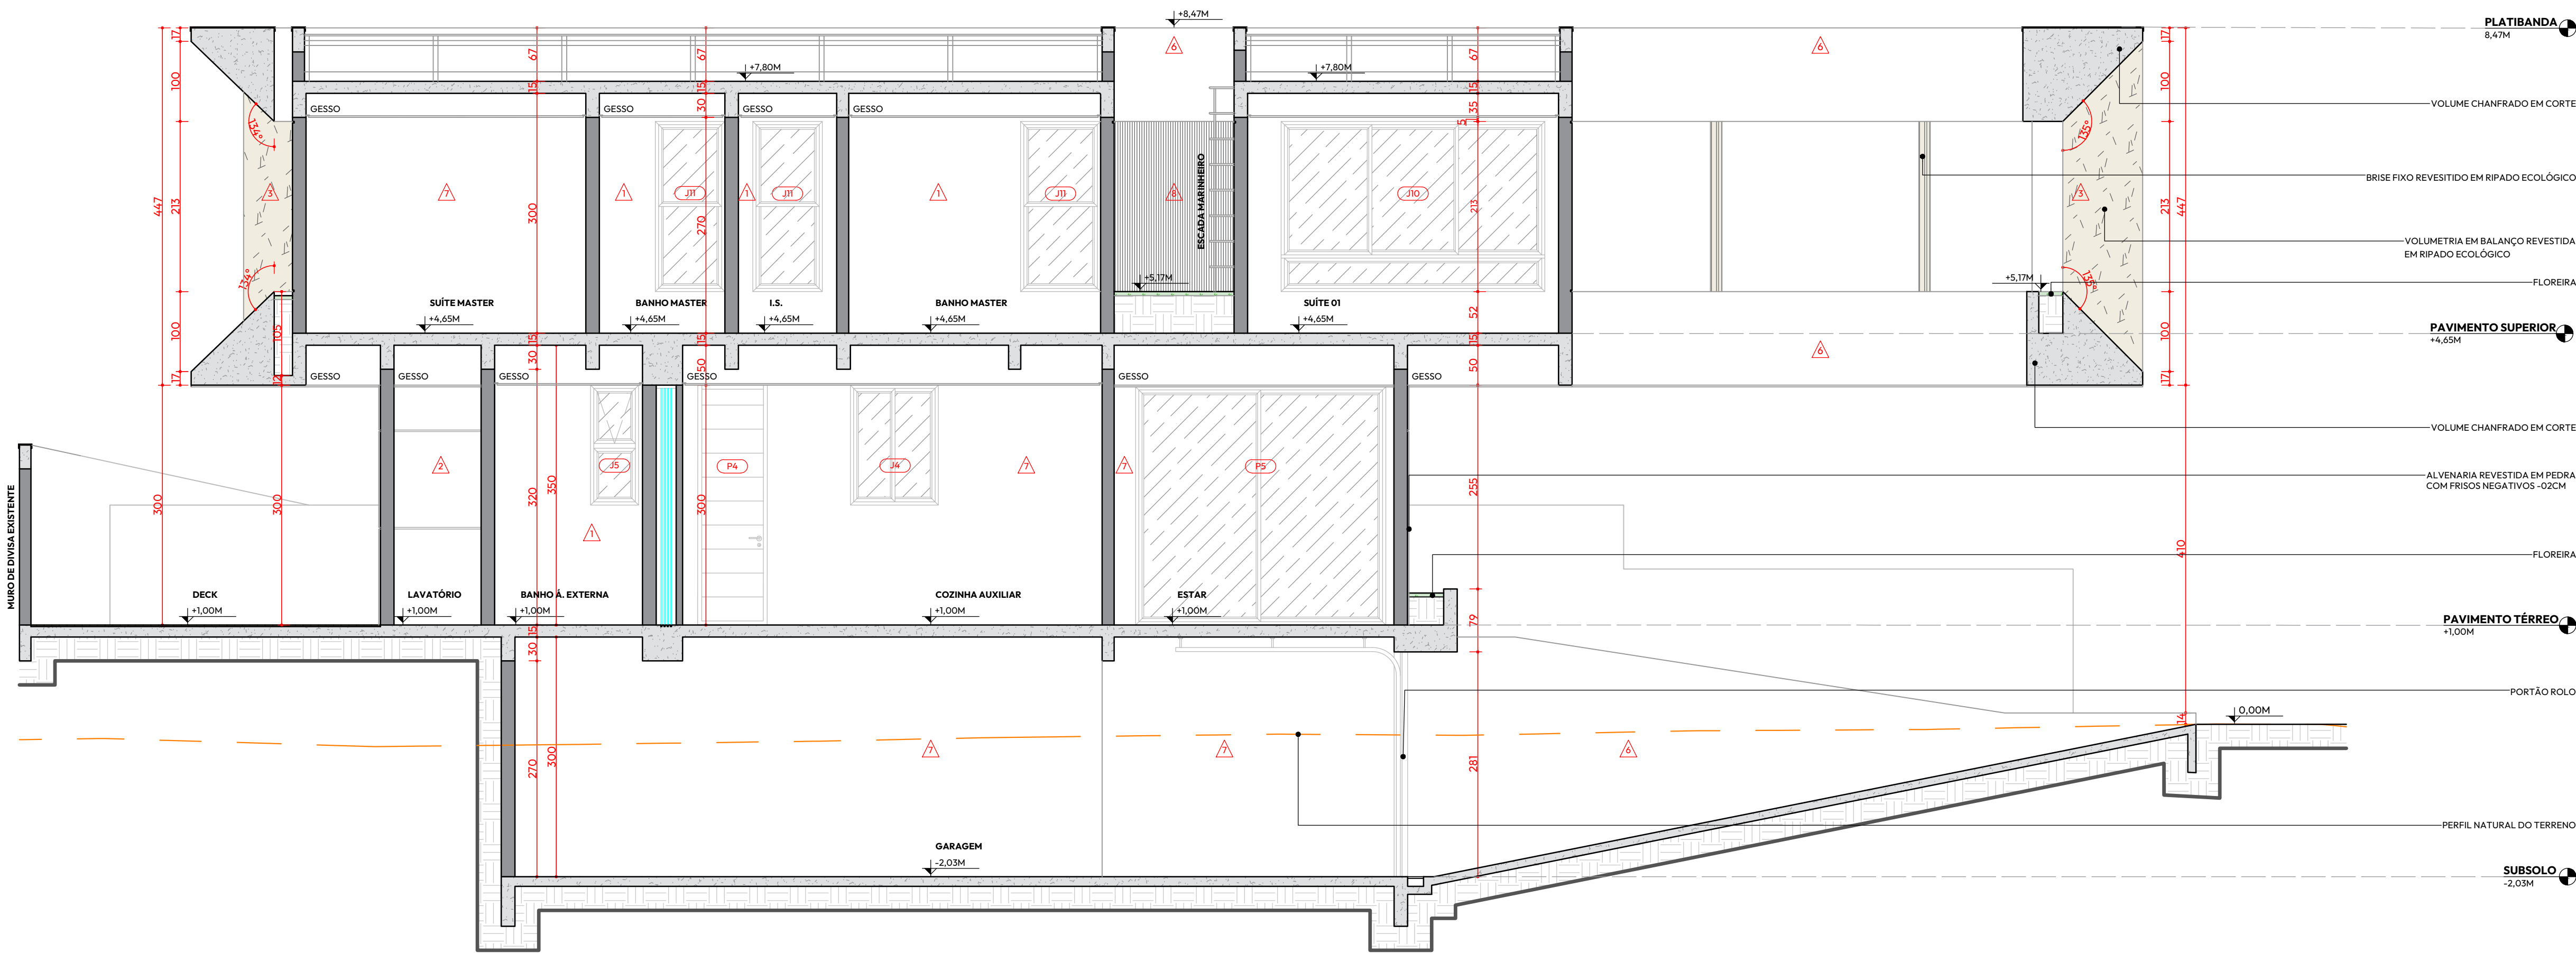

11 CORTEE/E
ESCALA: 1/50

- OBSERVAÇÕES DIVERSAS
- CONSIDERAR NICHOS PARA BANHEIRA E ARMARIOS E AÉREOS.
 - CONSIDERAR NICHOS PARA LAVAS-LOUÇAS E INCINERAS E ESPAÇOS GOURMETS.
 - CONSIDERAR REBAIXO DE 2 CM EM ÁREAS DE BOX DOS BANHEIROS.
 - CONSIDERAR VENGIA E CONTRAVENGIA EM TODAS AS ABERTURAS.
 - CONSIDERAR IMPERMEABILIZAÇÃO EM BANHEIROS, BALCÕES, LAJES APARENTES, SACADAS, FLOREIRAS E DEMAS ÁREAS INDICADAS PELO RESPONSÁVEL PELA EXECUÇÃO.
 - CONSIDERAR RODAPÊ EMBUTIDO EM TODOS OS PAVIMENTOS.
 - CONSIDERAR INCLINAÇÃO DE NO MÍNIMO 2% E DRENOS EM ÁREAS DE LAJES IMPERMEABILIZADAS E TERRAÇOS.
 - DEIXAR ESPERA ELÉTRICA PARA ILUMINAÇÃO DE JARDIM.
 - QUALQUER DIVERGÊNCIA DEVE SER COMPATIBILIZADA ANTES DA EXECUÇÃO.
 - OS MUIROS DE DIVISA DEVEM INICIAR A PARTIR DA FAIXA DE RECVO FRONTAL (3 METROS)
 - A ALTURA MÁXIMA DOS MUIROS EM RELAÇÃO AO PERFIL MODIFICADO DO TERRENO OU DO ARRIMO NÃO DEVE ULTRAPASSAR 2 METROS.
 - A TOPOGRAFIA DA CALÇADA DEVE PERMANECER NO PERFIL NATURAL.
 - A CALÇADA DEVE SER EXECUTADA CONFORME PADRÃO ESTABELECIDO PELO CONDOMÍNIO.
 - TODAS AS CONDENSADORAS DEVEM SER POSICIONADAS NA SACADA TÉCNICA JUNTO AO TELHADO. É ESTRITAMENTE PROIBIDO O POSICIONAMENTO EM FACHADAS.

TABELA DE ACABAMENTOS DE PISO	
SIMBOLOGIA	DESCRIÇÃO
1	PORCELANATO
2	MÁRMORE ESCOVADO
3	MADERA ECOLÓGICA
4	VINÍLICO COLADO
5	CONCRETO BRUTO
6	LAJE IMPERMEABILIZADA

TABELA DE ACABAMENTOS DE PAREDE	
SIMBOLOGIA	DESCRIÇÃO
1	PORCELANATO
2	MÁRMORE ESCOVADO
3	PINTURA PROJETADA ESPECIAL
4	PINTURA ACRILICA EXTERNA BRANCA A DEFINIR
5	CONCRETO BRUTO
6	PINTURA ACRILICA EXTERNA MARROM A DEFINIR
7	PINTURA ACRILICA INTERNA A DEFINIR
8	BRISÉ/ ANTEPARO EM SERRALHERIA

TABELA DE ACABAMENTOS DE TETO	
SIMBOLOGIA	DESCRIÇÃO
1	MADERA ECOLÓGICA
2	GESSO EM PINTURA ACRILICA A DEFINIR
3	LAJE EM PINTURA ACRILICA A DEFINIR

TABELA DE ESQUADRIAS - PORTAS					
SIMBOLO	TAMANHO	VÃO	SISTEMA	ACABAMENTO	QUANTIDADE
P1	126X300CM	126X300CM	PIVOTANTE - PISO TETO	BEGE	01 UN
P2	80X300CM	87X300CM	GIRO - PISO TETO	BEGE	02 UN
P3	-	CONFERIR	PORTA L. MÃO ANGA TELHADO EMBUTIDO PISO	PRETO	01 UN
P4	80X300CM	87X300CM	GIRO - PISO TETO	ALUM. BEGE C/ FRISOS	03 UN
P5	313X300CM	313X300CM	GIRO - PISO TETO	ALUM. VIDRO PRETA	01 UN
P6	103X270CM	103X270CM	CORRER - PISO TETO	ALUM. VIDRO MARROM	01 UN
P7	80X270CM	87X270CM	CORRER - PISO TETO	A DEFINIR	03 UN
P8	80X100CM	87X100CM	GIRO	ALUM. MARROM C/ VENEZ.	02 UN
P9	80X270CM	87X270CM	GIRO	PVC BRANCO	02 UN
P10	100X200CM	100X200CM	CORRER	PVC BRANCO	02 UN
P11	390X280CM	390X280CM	PORTÃO ROLÓ	MADERA RIP. ECOLÓGICA	01 UN
P12	80X270CM	87X270CM	GIRO	PVC BRANCO	05 UN

TABELA DE ESQUADRIAS - JANELAS				
SIMBOLO	TAMANHO	VÃO	SISTEMA	ACABAMENTO
J1	250X255/150CM	250X255/150CM	FIXA	ALUM. PRETO E VIDRO
J2	280X270/30CM	280X270/30CM	CORRER 03 FOLHAS	ALUM. PRETO E VIDRO
J3	120X270/30CM	120X270/30CM	MAXIMAR	ALUM. P. E VIDRO FOSCO
J4	120X150/150CM	120X150/150CM	CORRER 02 FOLHAS	ALUM. PRETO E VIDRO
J5	60X150/150CM	60X150/150CM	MAXIMAR	ALUM. P. E VIDRO FOSCO
J6	214X213/52CM	214X213/52CM	CORRER 03 FOLHAS	ALUM. PRETO E VIDRO
J7	300X213/52CM	300X213/52CM	CORRER 03 FOLHAS	ALUM. PRETO E VIDRO
J8	333X213/52CM	333X213/52CM	CORRER 03 FOLHAS	ALUM. PRETO E VIDRO
J9	150X120/150CM	150X120/150CM	CORRER 02 FOLHAS	ALUM. PRETO E VIDRO
J10	330X213/52CM	330X213/52CM	CORRER 03 FOLHAS	ALUM. PRETO E VIDRO
J11	100X213/52CM	100X213/52CM	CORRER 03 FOLHAS	ALUM. P. E VIDRO FOSCO
J12	87X213/52CM	87X213/52CM	CORRER 03 FOLHAS	ALUM. P. E VIDRO FOSCO
J13	200X213/52CM	200X213/52CM	CORRER 03 FOLHAS	ALUM. P. E VIDRO FOSCO
J14	400X213/52CM	400X213/52CM	CORRER 03 FOLHAS	ALUM. PRETO E VIDRO
J15	414X1313/565CM	414X1313/565CM	FIXA - 01 FOLHA	ALUM. PRETO E VIDRO
J16	1055X213/52CM	1055X213/52CM	FIXA - 04 FOLHAS	ALUM. PRETO E VIDRO
J17	220X80/130CM	220X80/130CM	CORRER 02 FOLHAS	ALUM. PRETO E VIDRO

REVISÕES:

REVISÃO	DATA	DESCRIÇÃO	DESENHO
R02	29/08/25	CORREÇÃO DO QUADRO DE ESTATÍSTICAS	JOSE
R03	29/09/25	CORREÇÃO DO QUADRO DE ESTATÍSTICAS	JOSE
R04	04/02/26	COMPATIBILIZAÇÃO DO PROJETO DE INTERIORES	JOSE

ESTATÍSTICAS:

ÁREA DO TERRENO	418,16M²	TAXA DE OCUPAÇÃO (177,24M²):	42,39%
ÁREA A CONSTRUIR TÊRREO	177,24M²	COEFICIENTE DE APROVEITAMENTO:	1,0153
ÁREA A CONSTRUIR SUPERIOR	122,24M²	TAXA DE PERMEABILIDADE:	38,94%
ÁREA A CONSTRUIR SUBSOLO	120,08M²	ESCADARIA ENTRADA (CONCRETO)	6,94M²
ÁREA TOTAL A CONSTRUIR	424,58M²	ÁREA DECK	11,88M²
ÁREA PERMEÁVEL	162,85M²	ÁREA PISCINA	38,09M²
SENDO:		ÁREA VARIANDA/ CALÇADAS/ BORDAS	26,99M²
CREMA:	113,15M²	ÁREA MURETAS	2,83M²
DRENANTE (85%)	58,48M²	ÁREA FLOREIRAS NÃO PERMEÁVEIS	4,57M²

ORGÃOS PÚBLICOS:

PROJETO ARQUITETÔNICO RESIDENCIAL

ARQUITETO:	GEOVANI CEZAR FELTRIN	CAU:	A130445-3
EXECUÇÃO:	MACIEL COSTA DA SILVA	CPF:	064.664.969-88
PROPRIETÁRIO:	MACIEL E FERNANDO		

LOCAL:	CONDOMÍNIO TERRAS ALPHA CASCAVEL, QUADRA 001/1, UNIDADE 16	ESCALA:	INDICADA	FOLHA:	EXE.04
CONTEÚDO:	CORTES D E	DESENHO:	JOSE		
		DATA:	09/04/25		EXE.05

A APROVAÇÃO DO PRESENTE PROJETO PELA PREFEITURA NÃO RECONHECE A PROPRIEDADE DO IMÓVEL

12 FACHADA LATERAL DIREITA - E.02
ESCALA: 1/50



- OBSERVAÇÕES DIVERSAS
- CONSIDERAR NICHOS PARA BANHEIRA E ARMÁRIOS E AÉREOS.
 - CONSIDERAR NICHOS PARA LAVAS-LOUÇAS E COZINHAS E ESPAÇOS GOURMETS.
 - CONSIDERAR REBAIXO DE 2 CM EM ÁREAS DE BOX DOS BANHEIROS.
 - CONSIDERAR VIGAS E CONTRAVIGAS EM TODAS AS ABERTURAS.
 - CONSIDERAR IMPERMEABILIZAÇÃO EM BANHEIROS, BALCÕES, LAJES, APARTELES, SACADAS, FLOREIRAS E DEMAIS ÁREAS INDICADAS PELO RESPONSÁVEL PELA EXECUÇÃO.
 - CONSIDERAR RODAPÉ EMBUTIDO EM TODOS OS PAVIMENTOS.
 - CONSIDERAR INCLINAÇÃO DE NO MÍNIMO 2% E DRENOS EM ÁREAS DE LAJES IMPERMEABILIZADAS E TERRAÇOS.
 - DEIXAR ESPERA ELÉTRICA PARA ILUMINAÇÃO DE JARDIM.
 - QUAL QUER DIVERGÊNCIA DEVE SER COMPATIBILIZADA ANTES DA EXECUÇÃO.
 - OS MUIROS DE DIVISA DEVEM INICIAR A PARTIR DA FAIXA DE RECUE FRONTAL (3 METROS)
 - A ALTURA MÁXIMA DO ARRIMO NÃO DEVE ULTRAPASSAR 2 METROS.
 - A TOPOGRAFIA DA CALÇADA DEVE PERMANECER NO PERFIL NATURAL.
 - A CALÇADA DEVE SER EXECUTADA CONFORME PADRÃO ESTABELECIDO PELO CONDOMÍNIO.
 - TODAS AS CONDENSADORAS DEVEM SER POSICIONADAS NA SACADA TÉCNICA AJUNTO AO TELHADO. É ESTRITAMENTE PROIBIDO O POSICIONAMENTO EM FACHADAS.

TABELA DE ACABAMENTOS DE PISO	
SIMBOLOGIA	DESCRIÇÃO
1	PORCELANATO
2	MÁRMORE ESCOVADO
3	MADERA ECOLÓGICA
4	VINILCO COLADO
5	CONCRETO BRUTO
6	LAJE IMPERMEABILIZADA

TABELA DE ACABAMENTOS DE PAREDE	
SIMBOLOGIA	DESCRIÇÃO
1	PORCELANATO
2	MÁRMORE ESCOVADO
3	PINTURA PROJETADA ESPECIAL
4	PINTURA ACRILICA EXTERNA BRANCA A DEFINIR
5	CONCRETO BRUTO
6	PINTURA ACRILICA EXTERNA MARRON A DEFINIR
7	PINTURA ACRILICA INTERNA A DEFINIR
8	BRISÉ/ ANTEPARO EM SERRALHERIA

TABELA DE ACABAMENTOS DE TETO	
SIMBOLOGIA	DESCRIÇÃO
1	MADERA ECOLÓGICA
2	GESSO EM PINTURA ACRILICA A DEFINIR
3	LAJE EM PINTURA ACRILICA A DEFINIR

TABELA DE ESQUADRIAS - PORTAS					
SÍMBOLO	TAMANHO	VÃO	SISTEMA	ACABAMENTO	QUANTIDADE
P1	126X300CM	126X300CM	PIVOTANTE - PISO TETO	BEGE	01 UN
P2	80X300CM	87X300CM	GIRO - PISO TETO	BEGE	02 UN
P3	-	CONFERIR	PORTA V. MÃO AMIGA TRILHO EMBUTIDO PISO	PRETO	01 UN
P4	80X300CM	87X300CM	GIRO - PISO TETO	ALUM. BEGE C/ FRISOS	03 UN
P5	313X300CM	313X300CM	GIRO - PISO TETO	ALUM. VIDRO PRETA	01 UN
P6	103X270CM	103X270CM	CORRER - PISO TETO	ALUM. VIDRO MARRON	01 UN
P7	80X270CM	87X270CM	CORRER - PISO TETO	A DEFINIR	03 UN
P8	80X100CM	87X100CM	GIRO	ALUM. MARRON C/ VENEZ.	02 UN
P9	80X270CM	87X270CM	GIRO	PVC BRANCO	02 UN
P10	120X210CM	120X210CM	CORRER	PVC BRANCO	02 UN
P11	390X280CM	390X280CM	PORTÃO ROLÔ	MADERA RIP. ECOLÓGICA	01 UN
P12	80X270CM	87X270CM	GIRO	PVC BRANCO	05 UN

TABELA DE ESQUADRIAS - JANELAS					
SÍMBOLO	TAMANHO	VÃO	SISTEMA	ACABAMENTO	QT.
J1	250X225/150CM	250X225/150CM	FIXA	ALUM. PRETO E VIDRO	01 UN
J2	280X270/30CM	280X270/30CM	CORRER 03 FOLHAS	ALUM. PRETO E VIDRO	01 UN
J3	120X270/30CM	120X270/30CM	MAXIM AR	ALUM. P. E VIDRO FOSCO	01 UN
J4	120X150/150CM	120X150/150CM	CORRER 02 FOLHAS	ALUM. PRETO E VIDRO	01 UN
J5	60X150/150CM	60X150/150CM	MAXIM AR	ALUM. P. E VIDRO FOSCO	01 UN
J6	214X213/52CM	214X213/52CM	CORRER 03 FOLHAS	ALUM. PRETO E VIDRO	01 UN
J7	300X213/52CM	300X213/52CM	CORRER 03 FOLHAS	ALUM. PRETO E VIDRO	01 UN
J8	333X213/52CM	333X213/52CM	CORRER 03 FOLHAS	ALUM. PRETO E VIDRO	01 UN
J9	150X120/150CM	150X120/150CM	CORRER 02 FOLHAS	ALUM. PRETO E VIDRO	01 UN
J10	330X213/52CM	330X213/52CM	CORRER 03 FOLHAS	ALUM. PRETO E VIDRO	01 UN
J11	100X213/52CM	100X213/52CM	CORRER 03 FOLHAS	ALUM. P. E VIDRO FOSCO	02 UN
J12	87X213/52CM	87X213/52CM	CORRER 03 FOLHAS	ALUM. P. E VIDRO FOSCO	02 UN
J13	200X213/52CM	200X213/52CM	CORRER 03 FOLHAS	ALUM. P. E VIDRO FOSCO	01 UN
J14	400X213/52CM	400X213/52CM	CORRER 03 FOLHAS	ALUM. PRETO E VIDRO	01 UN
J15	114X1313/565CM	114X1313/565CM	FIXA - 01 FOLHA	ALUM. PRETO E VIDRO	01 UN
J16	105X213/52CM	105X213/52CM	FIXA - 04 FOLHAS	ALUM. PRETO E VIDRO	01 UN
J17	220X80/130CM	220X80/130CM	CORRER 02 FOLHAS	ALUM. PRETO E VIDRO	01 UN



REVISÕES:

REVISÃO	DATA	DESCRIÇÃO	DESENHO
R02	29/08/25	CORREÇÃO DO QUADRO DE ESTATÍSTICAS	JOSÉ
R03	29/09/25	CORREÇÃO DO QUADRO DE ESTATÍSTICAS	JOSÉ
R04	04/02/26	COMPATIBILIZAÇÃO DO PROJETO DE INTERIORES	JOSÉ

ESTATÍSTICAS:

ÁREA DO TERRENO	418,16M²	TAXA DE OCUPAÇÃO (177,24M²):	42,39%
ÁREA A CONSTRUIR TERREO	177,24M²	COEFICIENTE DE APROVEITAMENTO:	1,0153
ÁREA A CONSTRUIR SUPERIOR	122,24M²	TAXA DE PERMEABILIDADE:	38,94%
ÁREA A CONSTRUIR SUBSÓLO	120,08M²	ÁREA DECK	6,94M²
ÁREA TOTAL A CONSTRUIR	424,58M²	ESCADARIA ENTRADA (CONCRETO)	11,88M²
ÁREA PERMEÁVEL	162,85M²	ÁREA PISCINA	38,09M²
SENDO:		ÁREA VARIADA/ CALÇADAS/ BORDAS	26,99M²
GRAMA:	113,15M²	ÁREA MURETAS	2,83M²
DRENANTE (85%)	58,48M²	ÁREA FLOREIRAS NÃO PERMEÁVEIS	4,57M²

ORGÃOS PÚBLICOS:

PROJETO ARQUITETÔNICO RESIDENCIAL

ARQUITETO: GEOVANI CEZAR FELTRIN CAU: A130445-3

EXECUÇÃO: MACIEL COSTA DA SILVA CPF: 064.664.969-88

PROPRIETÁRIO: MACIEL E FERNANDO

LOCAL: CONDOMÍNIO TERRAS ALPHA CASCAVEL, QUADRA 001, UNIDADE 16

CONTEÚDO: FACHADAS/ ELEVACOES


ESCALA: INDICADA

FOLHA: EXE.05


DATA: 09/06/25

A APROVAÇÃO DO PRESENTE PROJETO PELA PREFEITURA NÃO RECONHECE A PROPRIEDADE DO IMÓVEL

13 FACHADA LATERAL ESQUERDA - E.04
ESCALA: 1/50

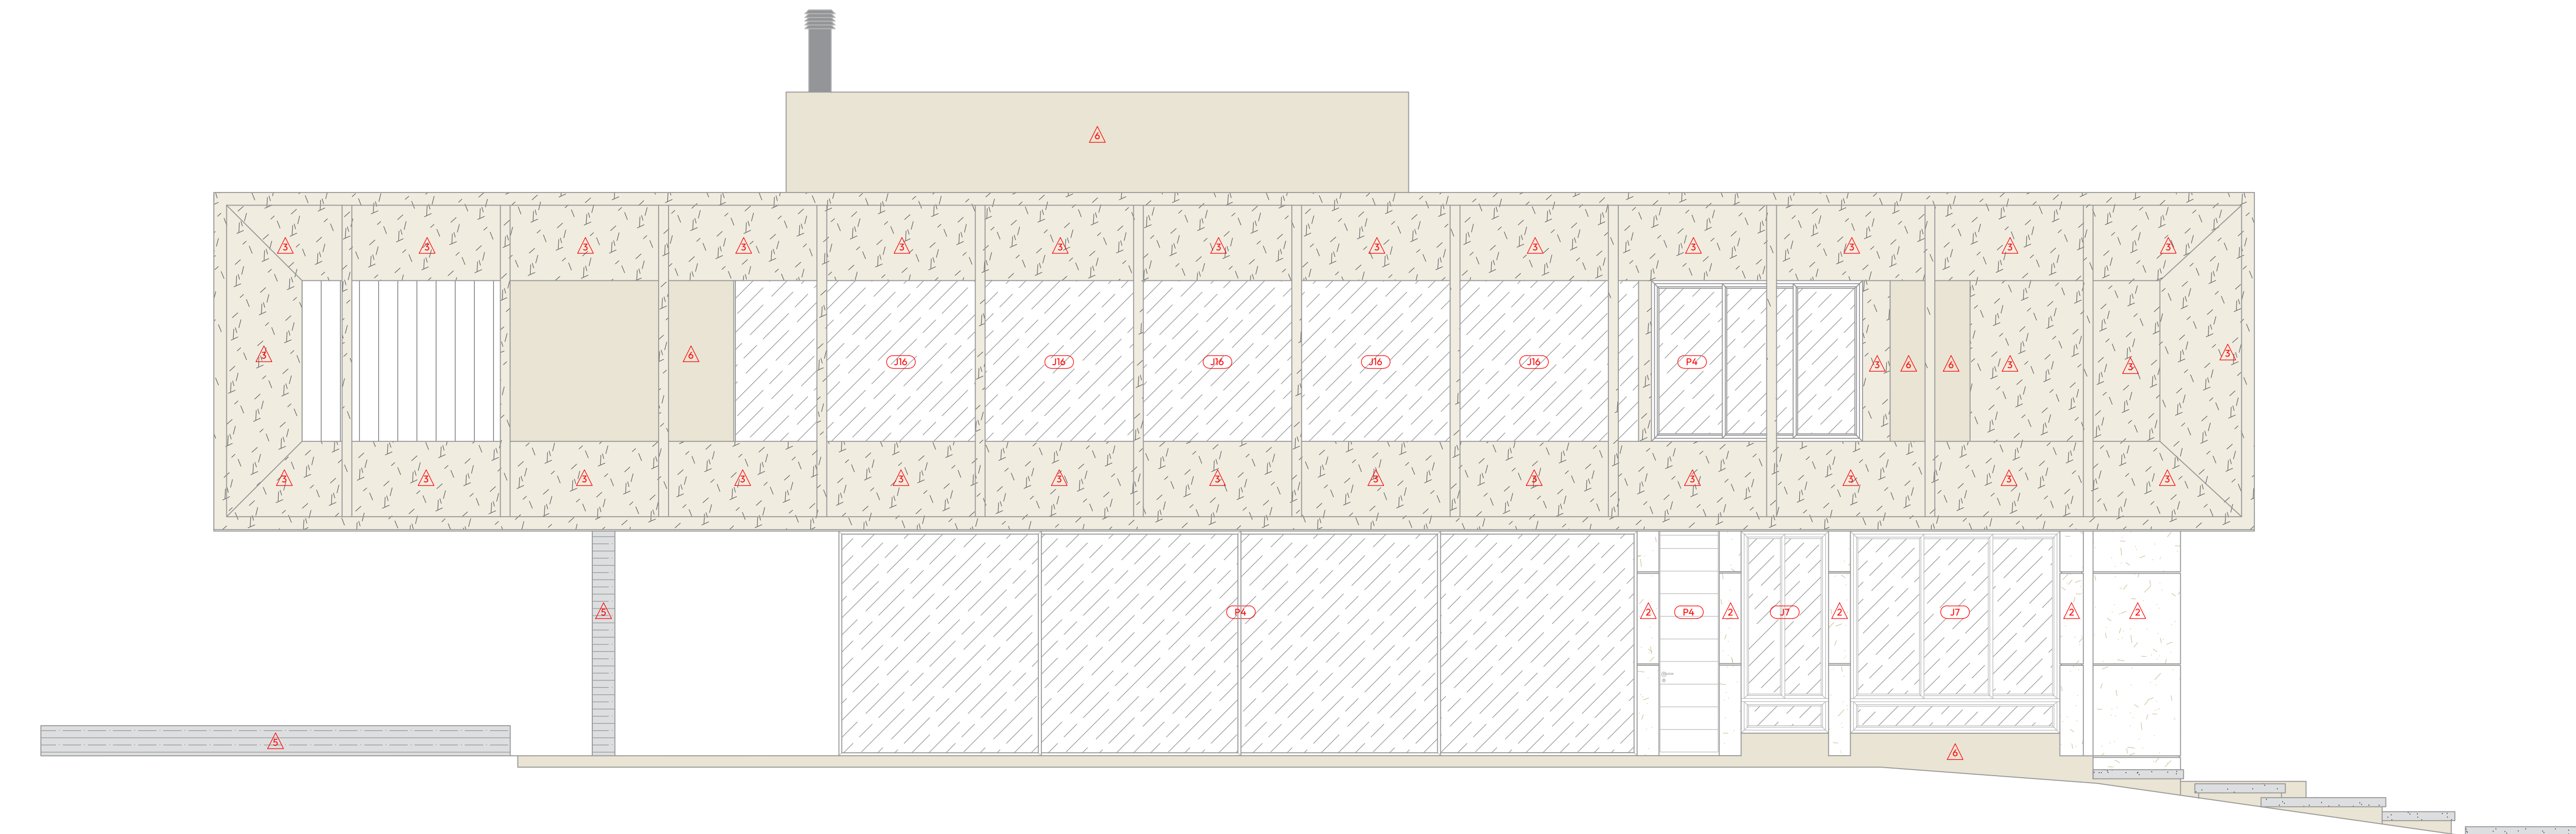

14 FACHADA POSTERIOR - E.03
ESCALA: 1/50

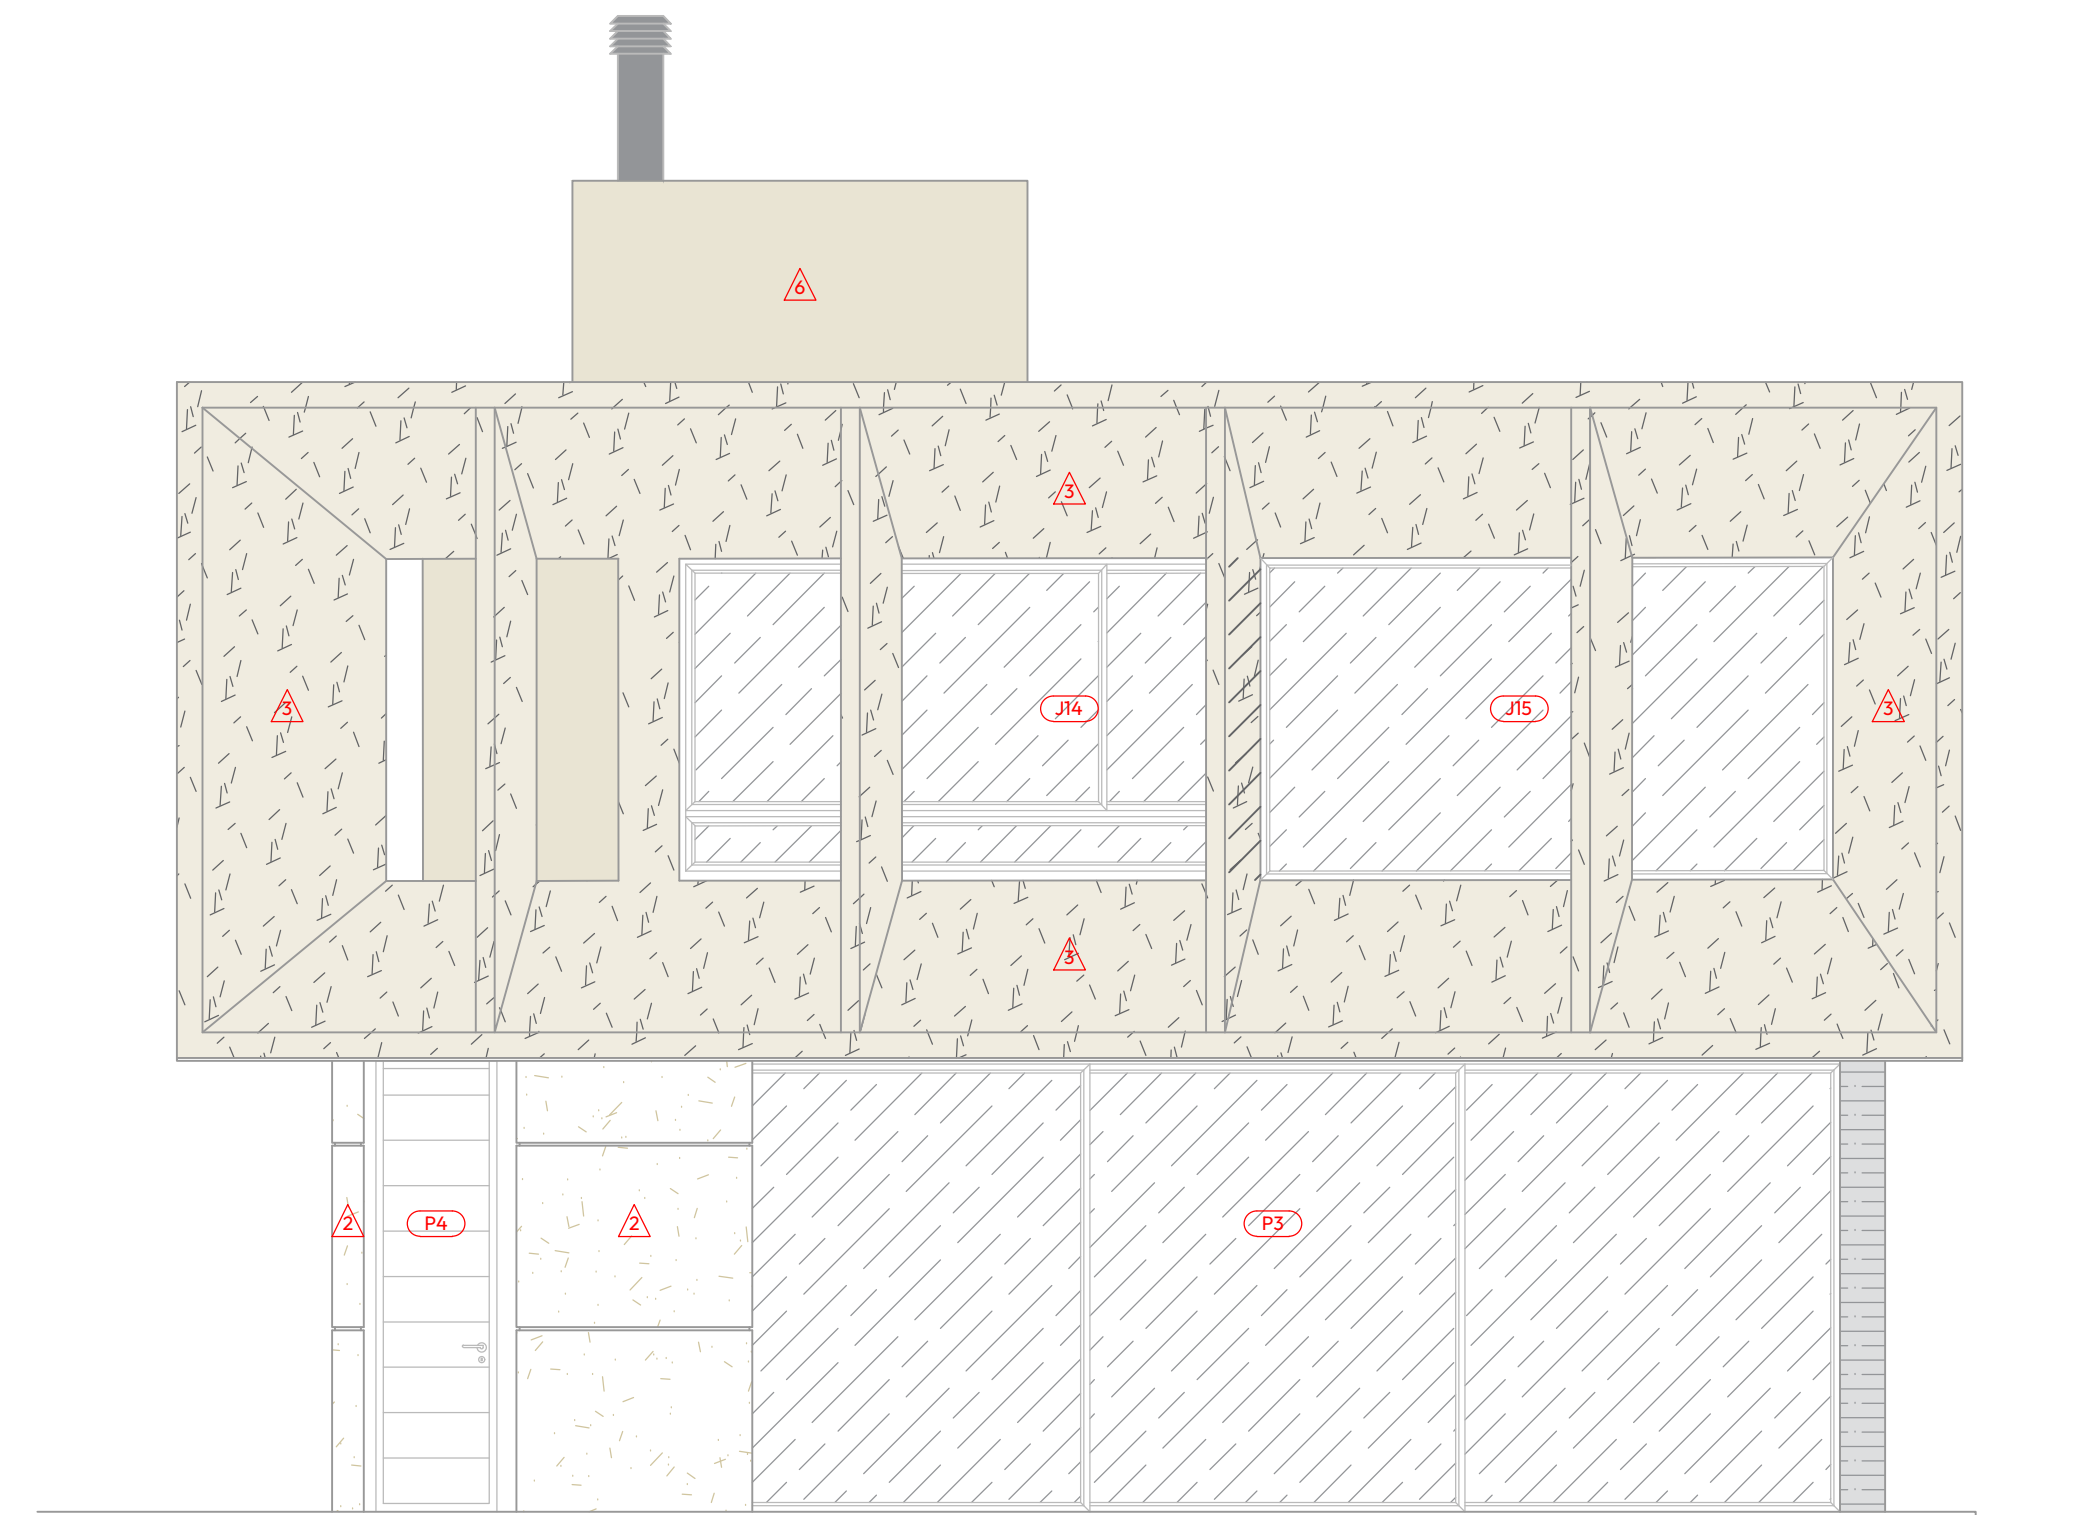

15 FACHADA FRONTAL - E.01
ESCALA: 1/50

